


EXISTING	PROPOSED	DESCRIPTION	EXISTING	PROPOSED	DESCRIPTION
		EDGE OF PAVEMENT			REDUCER
		CURB AND GUTTER			FENCE
		EDGE OF GRAVEL			DITCH/SWALE
		TOP/BOTTOM OF BANK			WATERMAIN (SIZE AND MATERIAL NOTED)
		CATCH BASIN			SANITARY SEWER (SIZE AND MATERIAL NOTED)
		WATER VALVE			STORM DRAIN (SIZE AND MATERIAL NOTED)
		FIRE HYDRANT			UNDERGROUND TELEPHONE / COMMUNICATIONS
		CAPPED END			UNDERGROUND HYDRO
		UTILITY POLE AND STREET LIGHT (LABELED PP,TP,PP/LS ETC.)			GAS
		MANHOLE			MONUMENT
		CLEANOUT			PROPERTY LINE
		SANITARY/STORM INSPECTION CHAMBER (200# RISER)			CENTERLINE AND STATIONING
		JUNCTION BOX			ELEVATIONS
		AIR VALVE			PAVEMENT REMOVAL
		WATER METER			NEW ASPHALT

LIST OF DRAWINGS

DWG No.	DESCRIPTION
C01	KEY PLAN, DRAWING LIST & GENERAL NOTES
C02	SITE SERVICING
C03	SITE GRADING
C04	DETAILS
C05	STORM WATER MANAGEMENT PLAN
C06	EROSION & SEDIMENT CONTROL PLAN

ELECTRICIA DRAWINGS (PREPARED BY RB ENGINEERING)

E1.01	SITE PLAN ELECTRICAL LAYOUT
E3.02	ELECTRICAL DETAILS
E4.01	ELECTRICAL SPECIFICATIONS

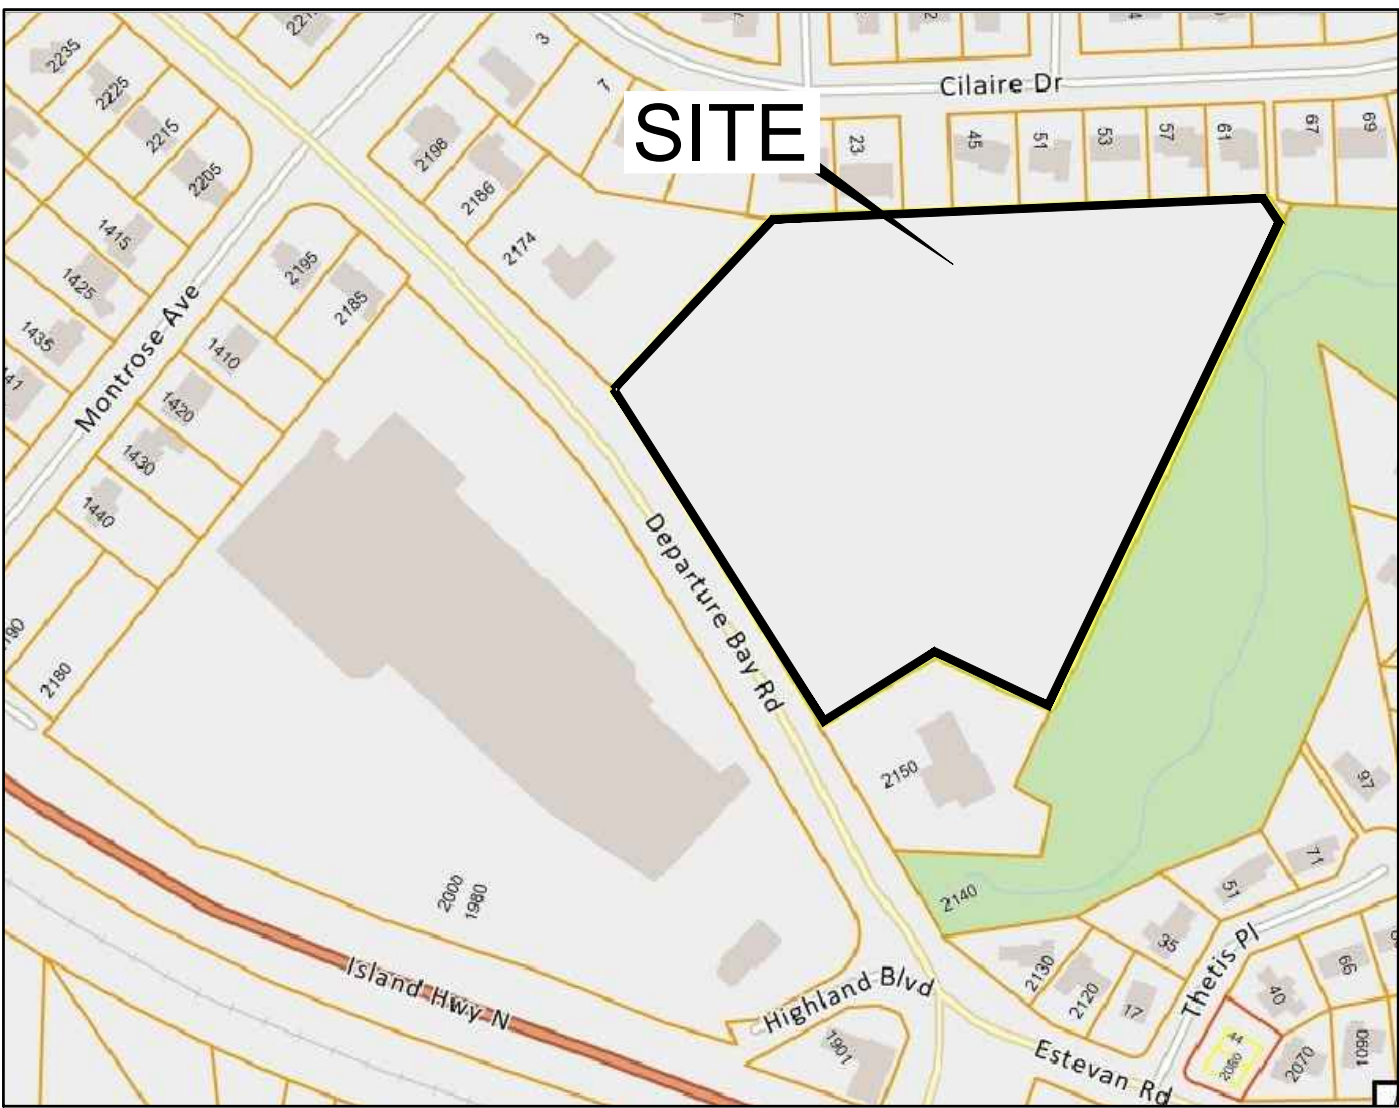

LOCATION PLAN
NTS

GENERAL NOTES:

- ALL WORK AND MATERIALS ARE TO BE AS DESCRIBED IN THE CITY OF NANAIMO ENGINEERING STANDARDS & SPECIFICATIONS LATEST EDITION (No. 14, JULY 2022) OR AS OTHERWISE APPROVED BY THE CITY ENGINEER.
- CONNECTION TO, OR ALTERATION OF, EXISTING CITY-OWNED UTILITIES, REQUIRES AUTHORIZATION BY THE CITY ENGINEER.
- A "PERMIT TO INSTALL WORKS WITHIN STREETS, LANES AND CITY PROPERTY AREAS" WILL BE REQUIRED WHERE CONSTRUCTION IS TO BE UNDERTAKEN IN CITY OF NANAIMO RIGHT-OF-WAYS AND/OR CITY OF NANAIMO-OWNED UTILITIES OR PROPERTIES.
- UPON APPROVAL OF THE PERMIT, THE CITY OF NANAIMO'S CONSTRUCTION DIVISION SHALL BE NOTIFIED 48 HOURS PRIOR TO COMMENCEMENT OF WORK.
- THE ENGINEER SHALL BE NOTIFIED 48 HOURS PRIOR TO COMMENCEMENT OF WORK.
- CONTRACTOR TO COMPLY WITH ALL APPLICABLE MINISTRY OF ENVIRONMENT AND DEPARTMENT OF FISHERIES & OCEANS CANADA REQUIREMENTS AT ALL TIMES DURING CONSTRUCTION.
- CONTRACTOR TO CONFIRM LOCATION OF EXISTING UTILITIES AT ALL CROSSINGS AND CONNECTIONS AND REPORT ANY DISCREPANCIES TO THE ENGINEER PRIOR TO CONSTRUCTION.
- CONTRACTOR TO CONFIRM THAT ELEVATION, LOCATION AND GRADIENT OF ASPHALT MATCH EXISTING PRIOR TO PLACEMENT OF ASPHALT OR CONCRETE.
- ALL TREES NOT BEING REMOVED IN THE CONSTRUCTION AREA SHALL BE PROTECTED.
- ADJUST ALL MANHOLES, WATER VALVES, HYDRO VAULTS, ETC. TO MATCH NEW CONSTRUCTION.
- ALL LOCATIONS AND ELEVATIONS OF EXISTING UTILITIES SHOWN ARE APPROXIMATE ONLY AND SHOULD BE CONFIRMED BY USE OF A PIPE LOCATOR AND MANUAL DIGGING. ALL OR ANY STRUCTURES NOT NECESSARILY SHOWN.
- ALL DISTURBED SURFACES TO BE RESTORED TO EXISTING CONDITION OR BETTER.
- ALL ELEVATIONS ARE TO GEODETIC DATUM AND ARE REFERENCED TO MONUMENT 77H5327 ON CILATRE DRIVE. ELEVATION = 55.375
- DATA SOURCES:
 - TOPOGRAPHIC SURVEY COMPLETED BY TURNER & ASSOCIATES LAND SURVEYING IN AUGUST, 2024
 - RECORD DRAWINGS PROVIDED BY THE CITY OF NANAIMO.

WATERMAIN NOTES:

- WHERE THE WATERMAIN IS WITHIN 3.0m HORIZONTALLY OR 0.45m VERTICALLY OF A STORM OR SANITARY SEWER, JOINTS ARE TO BE WRAPPED IN ACCORDANCE WITH ISLAND HEALTH AUTHORITY GUIDELINES.
- ALL WATERMAINS ARE TO BE PVC C900 DR18 (RATED TO 235 psi) WITH INTEGRALLY THICKENED BELL TO ASTM D3139, UNLESS OTHERWISE NOTED.
- A FULL LENGTH SECTION OF WATERMAIN PIPE IS TO BE INSTALLED DIRECTLY ADJACENT TO ALL FITTINGS WHERE APPLICABLE.
- ALL WATERMAIN FITTINGS TO HAVE BOTH JOINT RESTRAINTS AND THRUST BLOCKS.
- ALL MECHANICAL JOINT (MJ) RESTRAINTS TO BE UFR1500 OR EQUIVALENT.
- HANDLING, REMOVAL AND DISPOSAL OF ASBESTOS CEMENT PIPE TO BE AS PER CITY OF NANAIMO, WORKSAFE BC GUIDELINES, AND APPLICABLE REGULATORY REQUIREMENTS.
- THE PROJECT AREA IS LOCATED WITHIN PRESSURE ZONE 10 (HGL - 107m). BASED ON PIPE ELEVATIONS, APPROXIMATE MAX. WORKING PRESSURE IN THE MAIN TO BE 76 psi. TEST PRESSURE TO BE 200 psi MIN FOR ALL SERVICES.
- TRACER WIRE (14 GAUGE, BLUE IN COLOUR) SUITABLE FOR DIRECT BURY TO BE INSTALLED AS A CONTINUOUS LENGTH ALONG THE CENTERLINE OF THE SERVICE PIPE, AFFIXED TO THE TOP OF THE PIPE AT 1.0m INTERVALS. RUN WIRE FROM CORPORATION STOP TO METER BOX & COIL NEATLY AT TERMINAL POINTS WITH 600mm SURPLUS LENGTH. INSTALL AS PER MANUFACTURER'S RECOMMENDATIONS.
- ASPHALT APRONS PER CoN STD DWG No. W-9 ARE REQUIRED ON ALL VALVES NOT LOCATED IN PAVED AREAS.
- ALL TESTING (PRESSURE & BACTERIOLOGICAL) ARE TO BE COMPLETED & PASSED PRIOR TO CONNECTION TO CoN WATER SYSTEM.
- BACTERIOLOGICAL TESTING IS NOT REQUIRED ON THE FDC FIRELINE SERVICE.

STORM SEWER NOTES:

- ALL CATCH BASINS ARE TO BE PER CoN STD DWG No. SW-4 UNLESS OTHERWISE NOTED.
- ALL CATCH BASIN LEADS ARE TO BE 200# PVC SDR35 UNLESS OTHERWISE NOTED.
- ALL STORM SERVICES ARE TO BE 200# PVC SDR35 UNLESS OTHERWISE NOTED.
- ALL FITTINGS ARE TO BE MANUFACTURED PVC COMPONENTS.
- ALL BENDS ARE TO BE LONG-RADIUS.
- ALL GRAVITY STORM SEWERS ARE TO BE CCTV VIDEO REVIEWED & SENT TO THE ENGINEER FOR APPROVAL.

SANITARY SEWER NOTES:


- ALL SANITARY SERVICES ARE TO BE 150# PVC SDR28 UNLESS OTHERWISE NOTED.
- ALL FITTINGS ARE TO BE MANUFACTURED PVC COMPONENTS.
- ALL BENDS ARE TO BE LONG-RADIUS.
- ALL GRAVITY SANITARY SEWERS ARE TO BE CCTV VIDEO REVIEWED & SENT TO THE ENGINEER FOR APPROVAL.
- ALL SANITARY SEWERS ARE TO BE AIR PRESSURE TESTED PER CoN MoESS SECTION 6.62.6.

ROAD NOTES:

- ALL CURB AND GUTTER TO BE C.O.N. TYPE CS-1 UNLESS OTHERWISE NOTED.

PRIVATE UTILITY NOTES:

- PRIVATE UTILITY MAIN AND SERVICE LOCATIONS ARE APPROXIMATE ONLY AND ARE BASED ON BC ONE CALL INFORMATION.

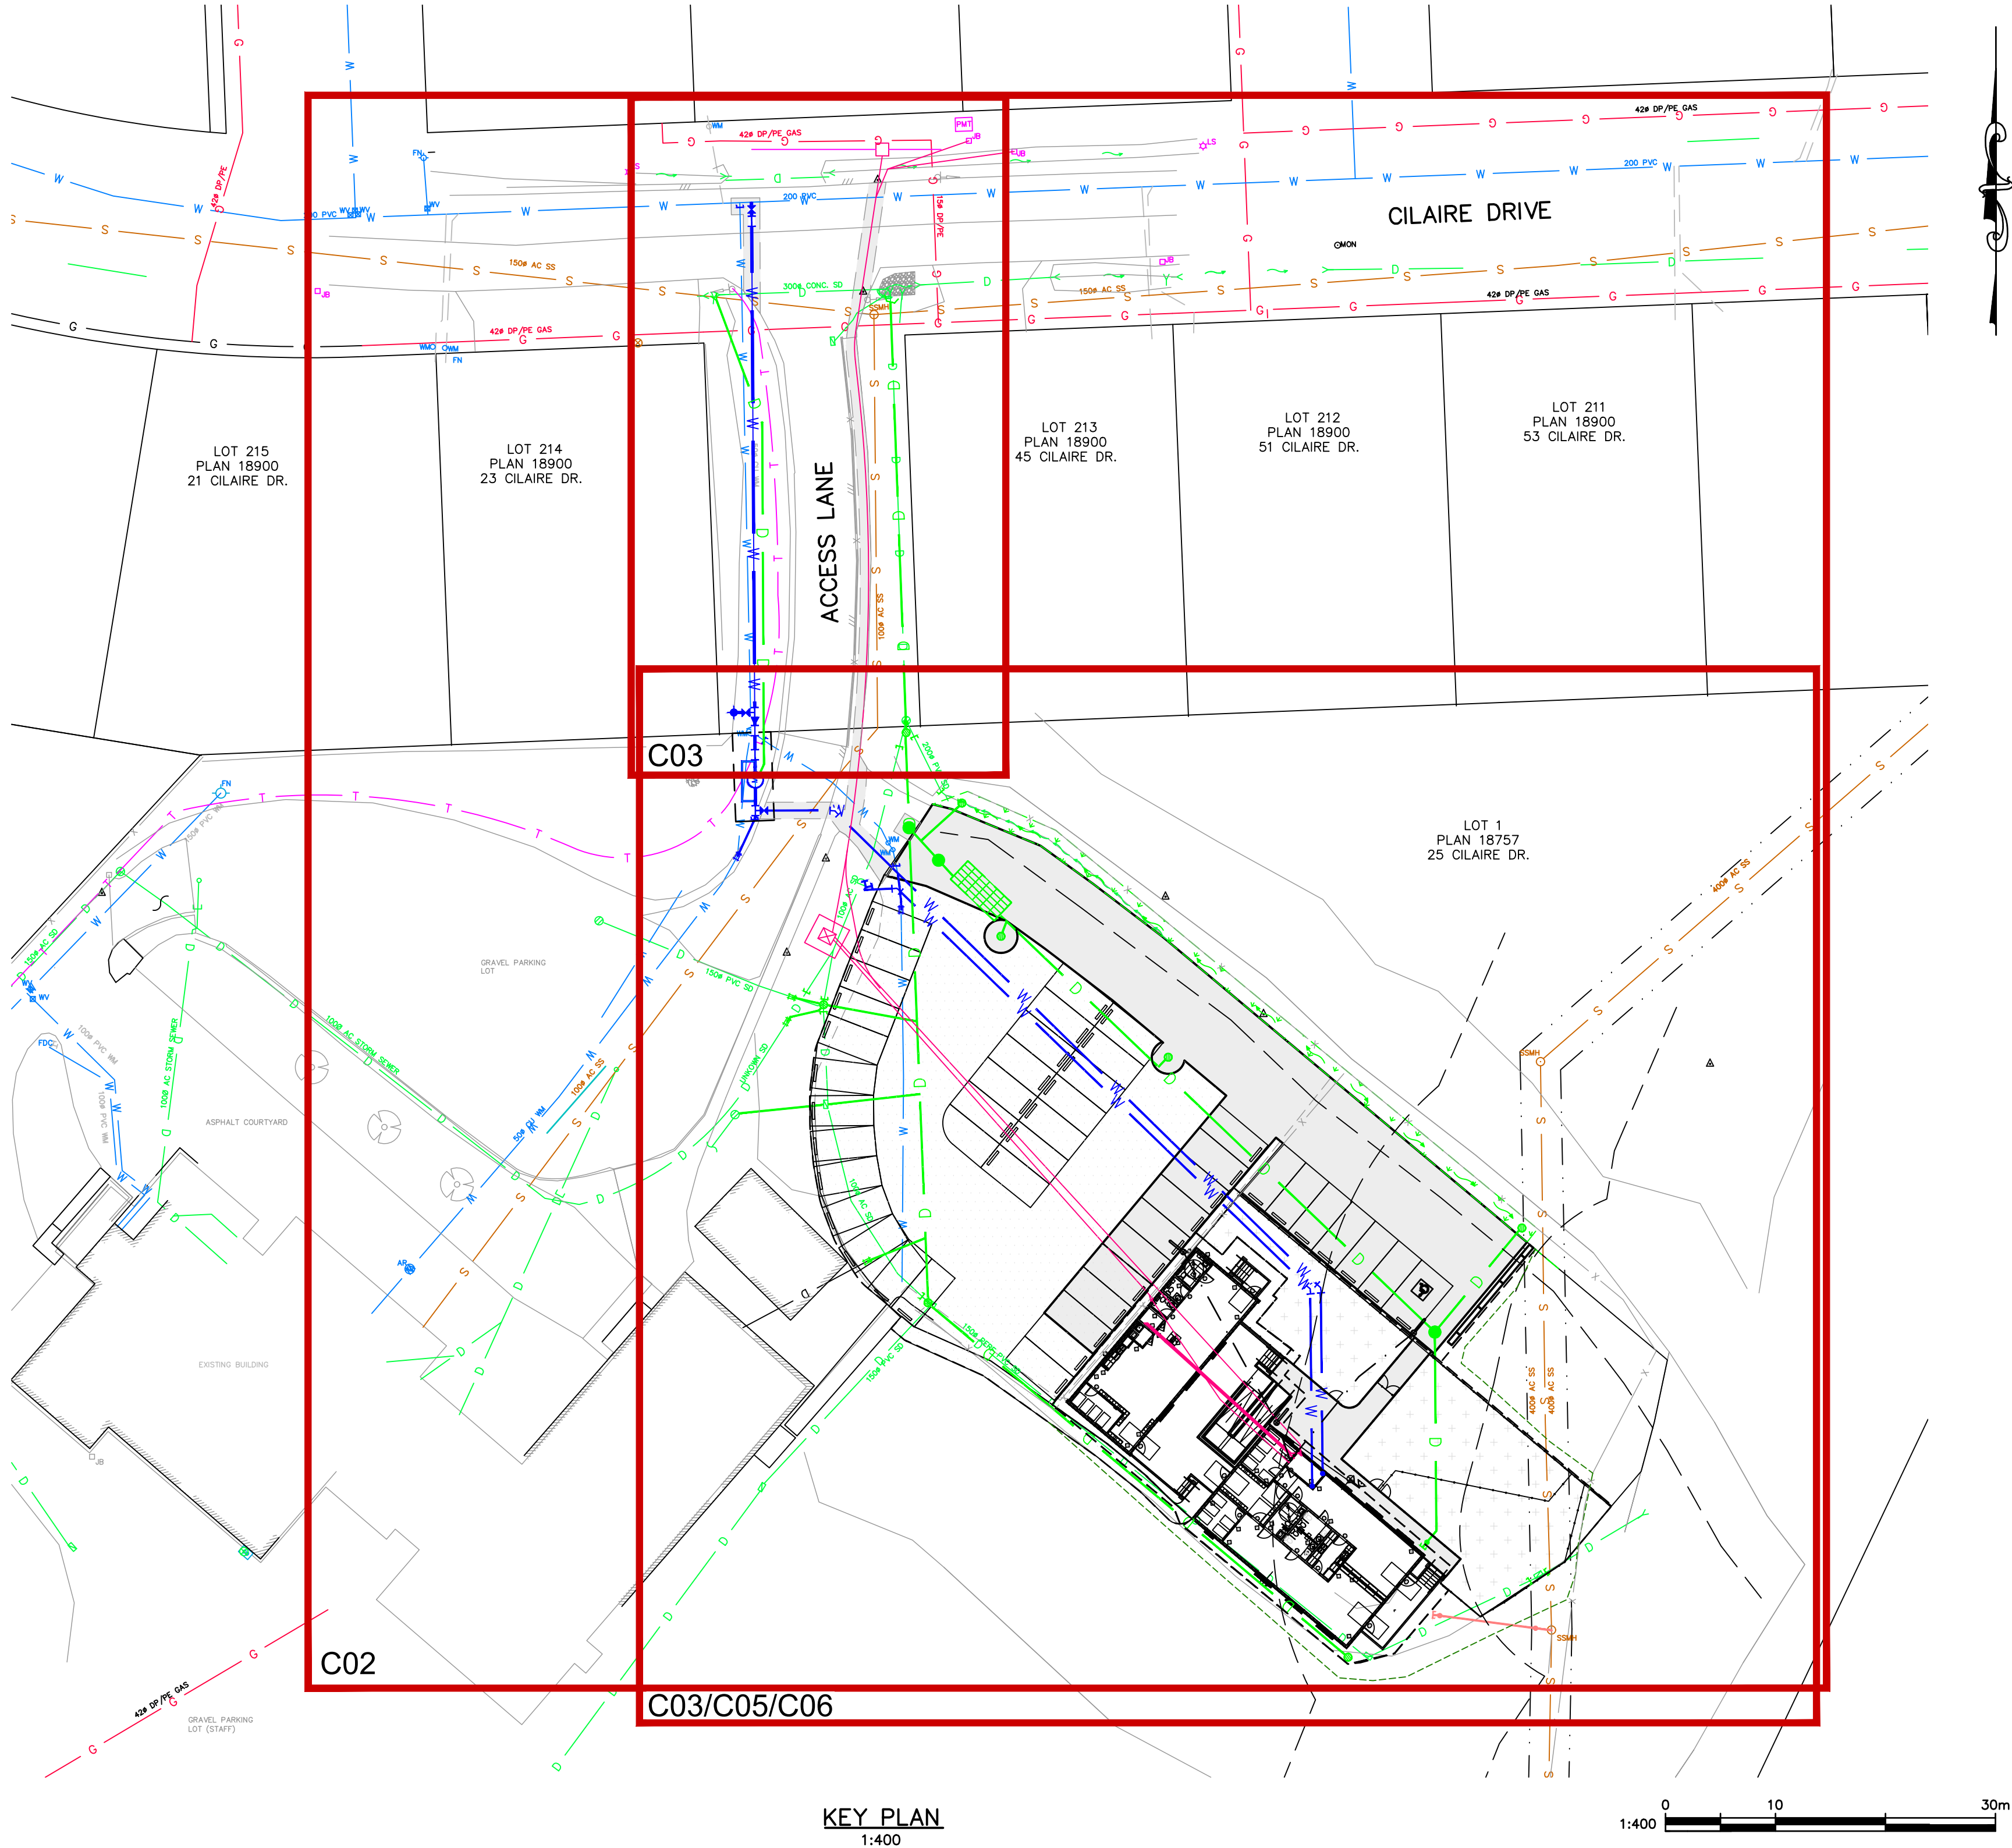

ISSUES		
No.	DATE	ISSUED FOR
A	2025.05.22	COORDINATION
B	2025.07.11	BUILDING PERMIT
C	2025.12.18	BUILDING PERMIT
D	2026.04.13	TENDER

NOT FOR
CONSTRUCTION

ISSUED FOR TENDER

CILATRE ELEMENTARY
MODULAR DAYCARE STUDIO
SITE WORKS

25 CILATRE DRIVE, NANAIMO, BC

SCHOOL DISTRICT 68 NANAIMO/LADYSMITH



HEROLD ENGINEERING
3701 Shenton Rd, Nanaimo, BC V9T 2H1
Tel: 250-751-8558 Fax: 250-751-8559
Email: mail@heroldengineering.com

©Copyright reserved. This drawing remains the exclusive property of Herold Engineering Limited and may not be reused or reproduced without written consent of Herold Engineering Limited.


KEY PLAN,
DRAWING LIST, &
GENERAL NOTES

DESIGNED SMJ	ENGINEER'S SEAL Permit to Practice No. 1000201	
DESIGN REVIEW PGR		
DRAFTED GV		
DRAFTING REVIEW PGR		
PROJECT No. 0016-352	CLIENT DRAWING No.	
SCALE H: 1:400 V: N/A	PERMIT No.	
HEL DRAWING No. C01	1 OF 6	REVISION D


File: H:\Projects\0016-352 Cilaire - Modular Daycare Studio\Civil\04C Drawings\0016-352 Civil Drawings.dwg Plot Time: Apr. 10, 2024 4:52 PM User: Scott Jensen

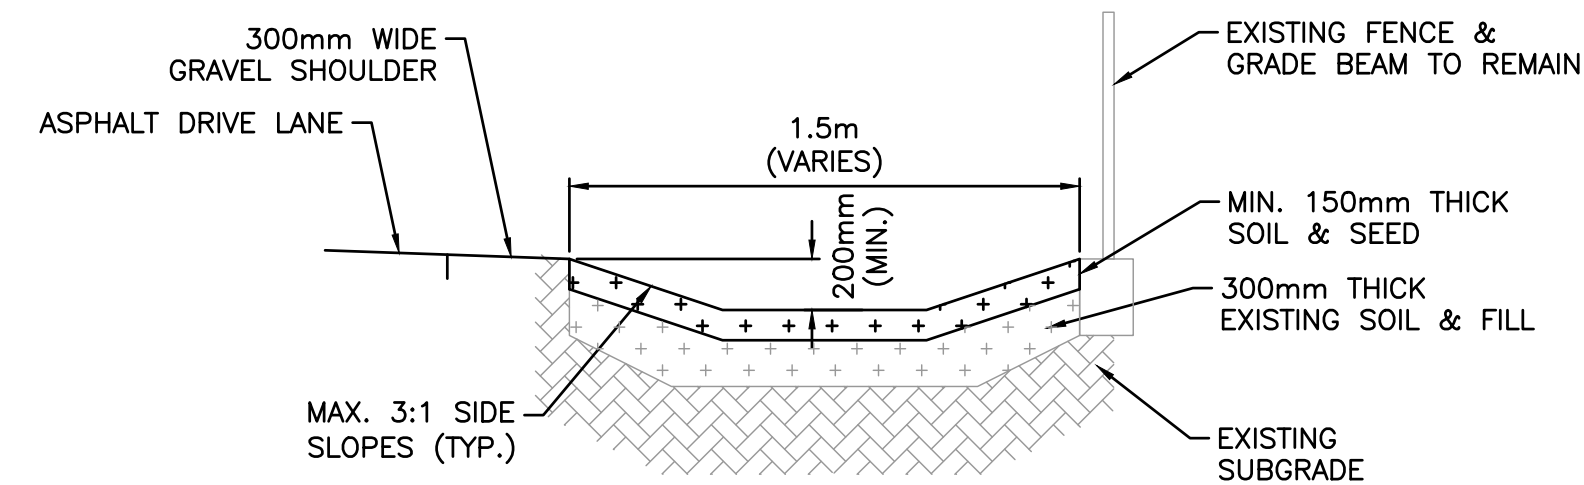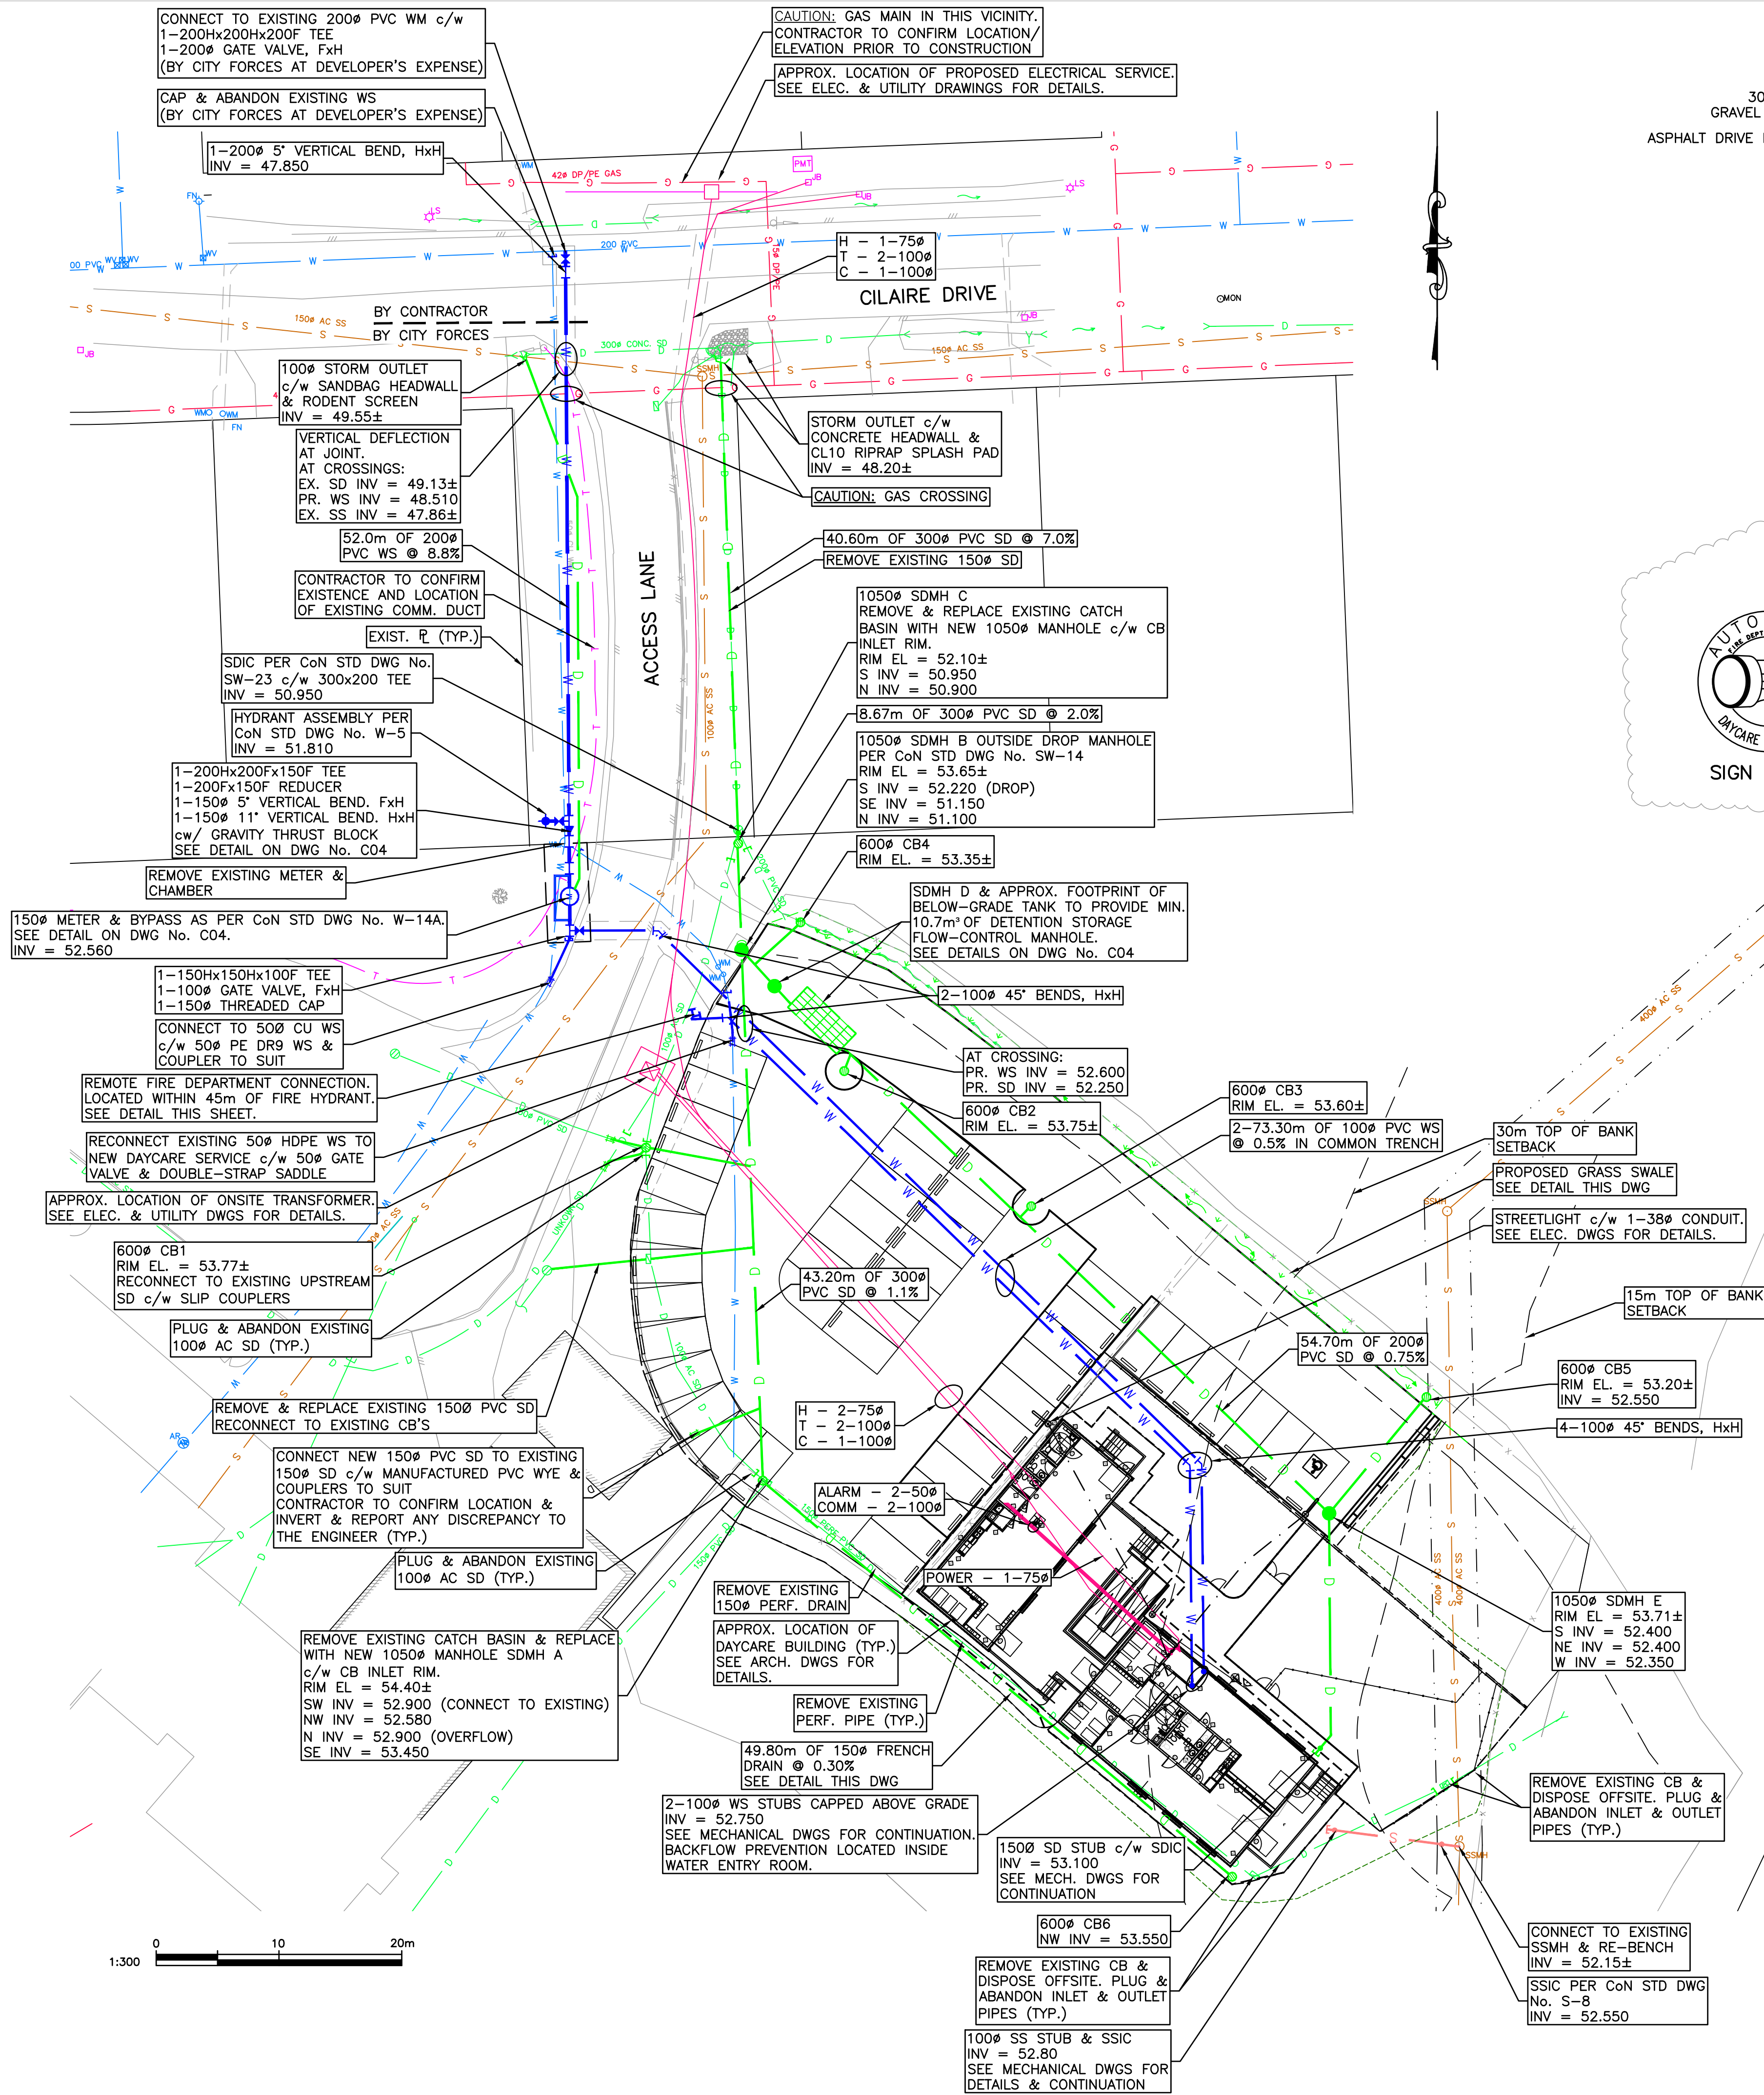

TYPICAL SWALE CROSS SECTION

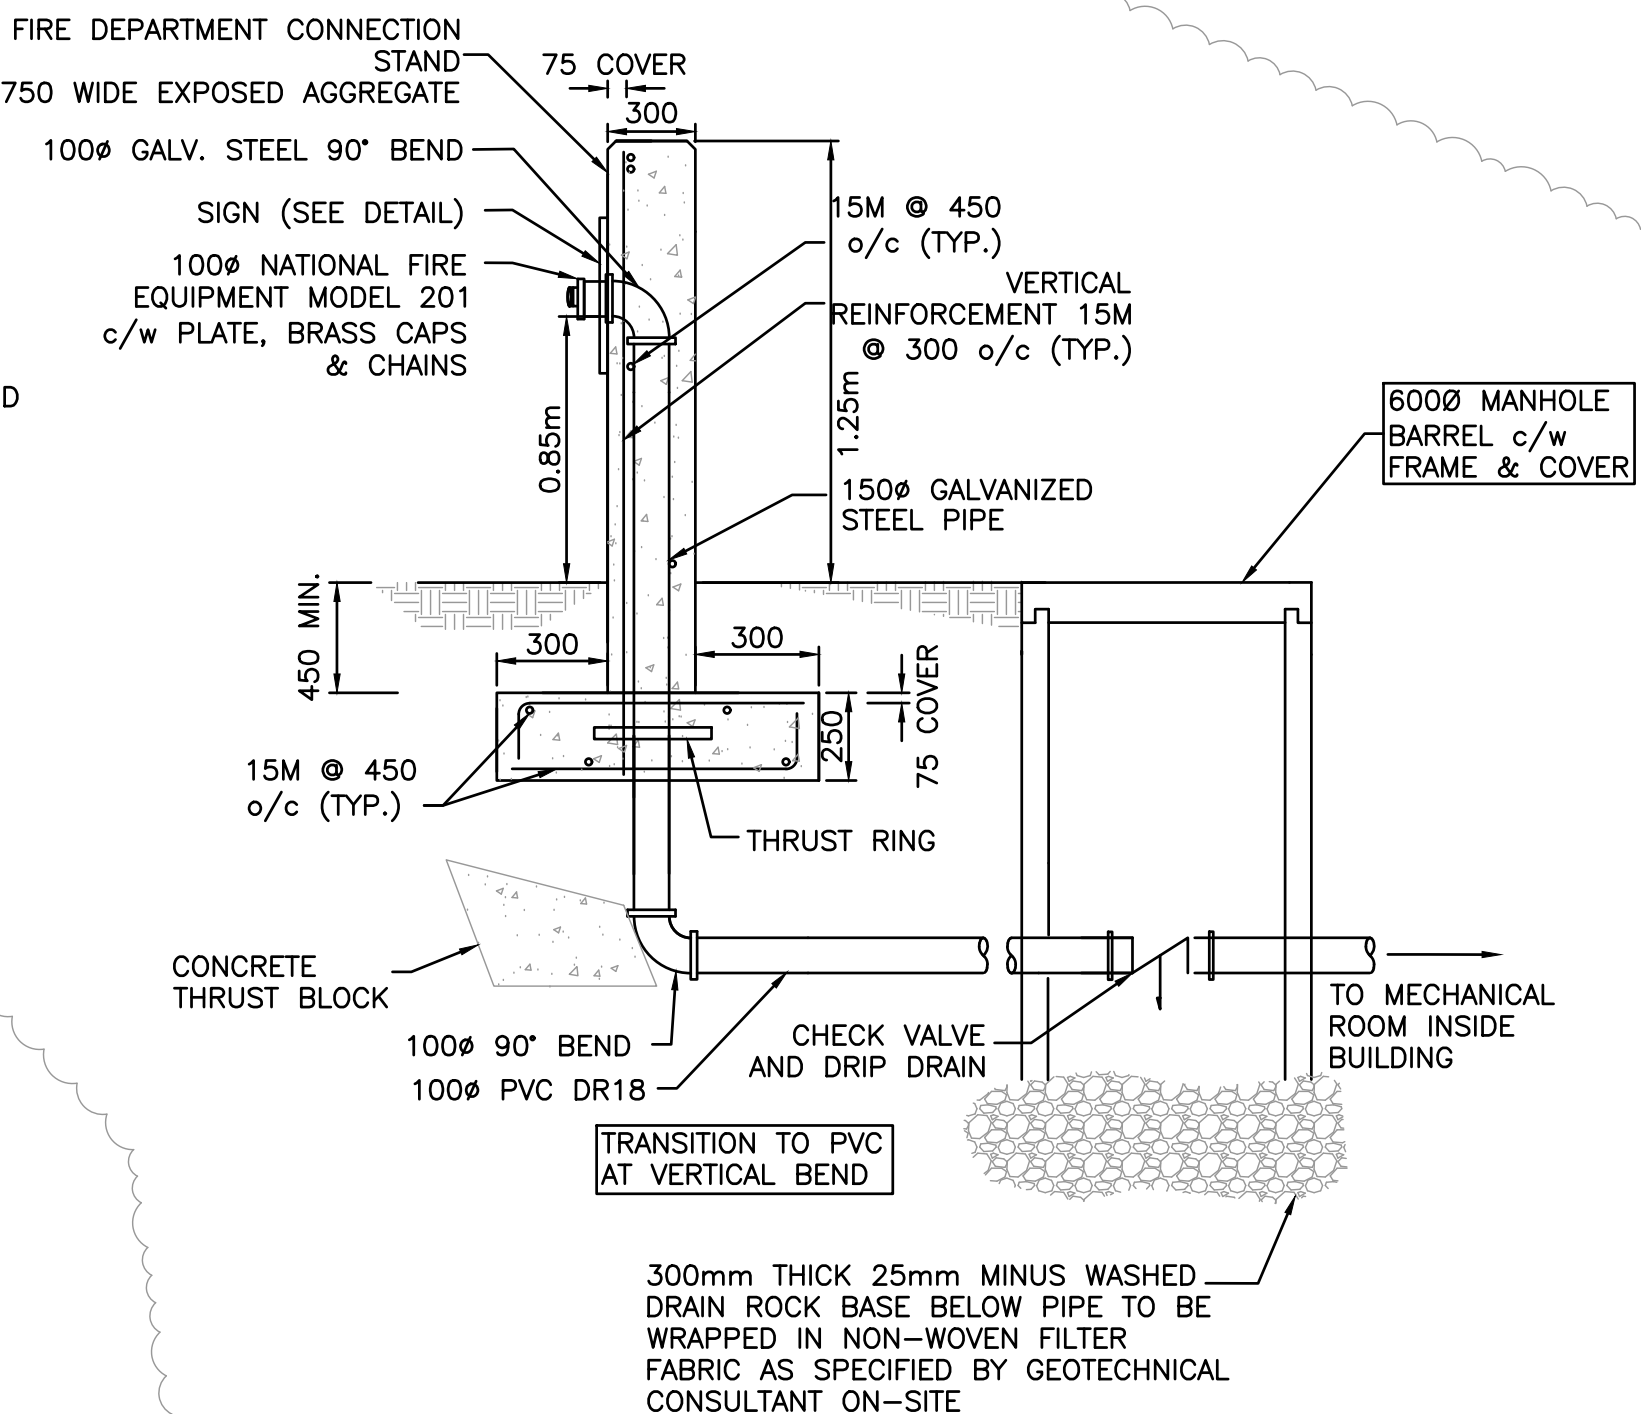

REMOTE SIAMESE FIRE DEPARTMENT CONNECTION DETAIL

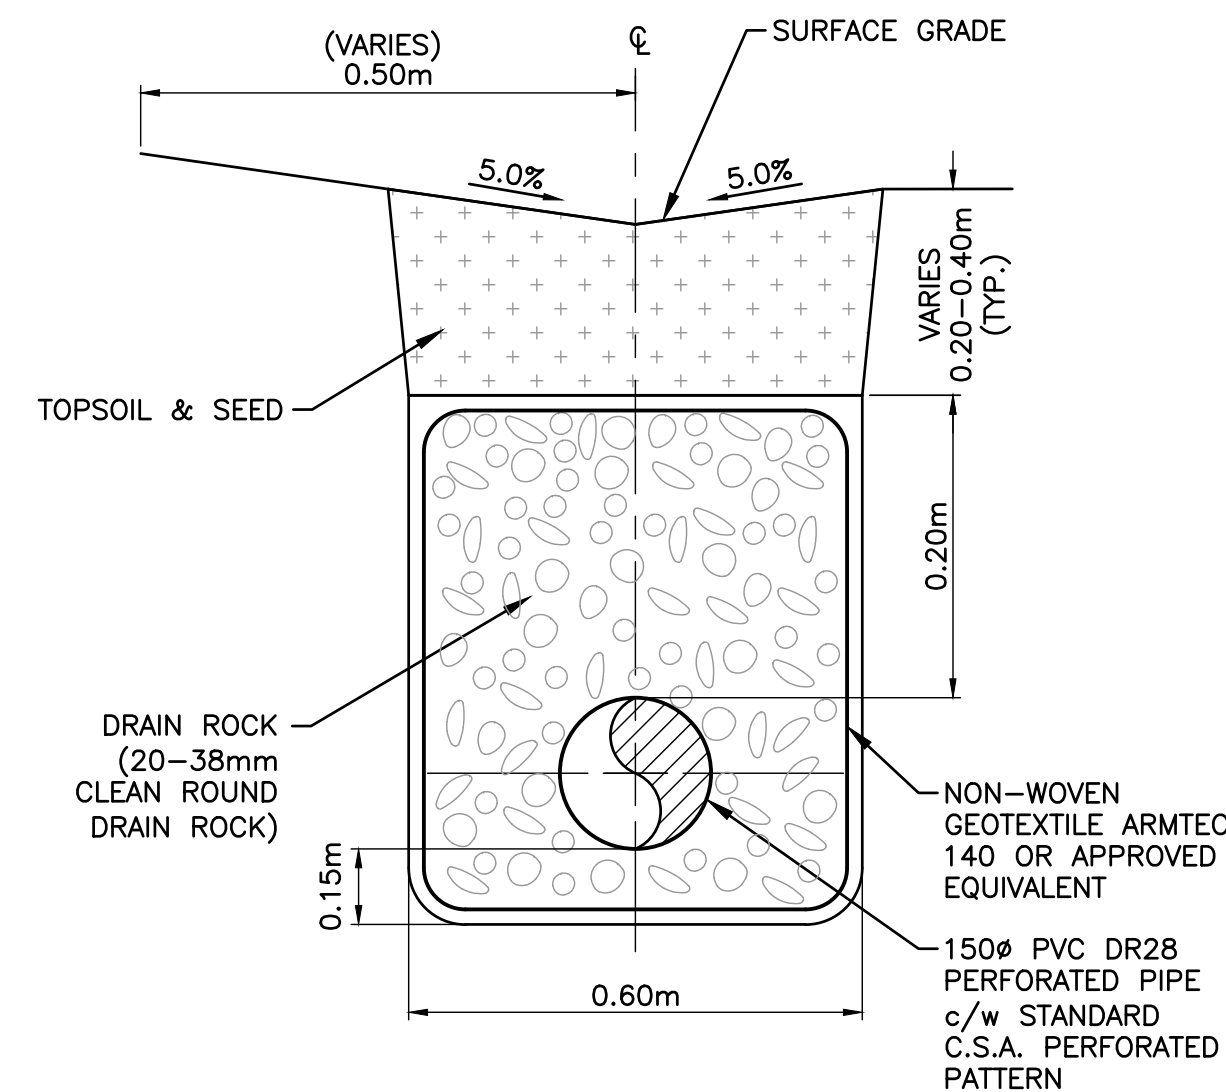

FRENCH DRAIN DETAIL

- NOTES:
- FOR GENERAL NOTES SEE DWG. No. C01.
 - SEE ELECTRICAL DRAWINGS PREPARED BY RB ENGINEERING & THIRD-PARTY UTILITY DRAWINGS FOR ELECTRICAL DETAILS.

ISSUES	
No.	DATE
A	2025.05.22
B	2025.07.11
C	2025.12.18
D	2026.04.13

NOT FOR CONSTRUCTION	
ISSUED FOR TENDER	

CILAIRE ELEMENTARY
MODULAR DAYCARE STUDIO
SITE WORKS

25 CILAIRE DRIVE, NANAIMO, BC

SCHOOL DISTRICT 68 NANIMO/LADYSMITH

HEROLD ENGINEERING


3701 Shenton Rd, Nanaimo, BC V9T 2H1
Tel: 250-751-8558 Fax: 250-751-8559
Email: mail@heroldengineering.com

©Copyright reserved. This drawing remains the exclusive property of Herold Engineering Limited and may not be reused or reproduced without written consent of Herold Engineering Limited.


SITE SERVICING	
DESIGNED SMJ	ENGINEER'S SEAL Permit to Practice No. 1000201
DESIGN REVIEW PGR	
DRAFTED GV	
DRAFTING REVIEW PGR	
PROJECT No. 0016-352	CLIENT DRAWING No.
SCALE H: 1:300 V: N/A	PERMIT No.
HEL DRAWING No. C02	REVISION D

File: H:\Projects\0016-352 Cilaire - Modular Daycare Studio\04C Drawings\0016-352 Civil Drawings.dwg Plot Time: Apr. 10, 2024 4:52 PM User: Scott Jensen

- STRUCTURAL PAD**
- 100mm GRANULAR BASE
 - 600mm GRANULAR SUBBASE*
 - (SEE GEOTECHNICAL REPORT)
- PLAY AREA**
- 150mm WOOD CHIPS (FUTURE - BY OTHERS)
 - 100mm GRANULAR BASE
 - 300mm GRANULAR SUBBASE*
- ASPHALT PAVING AREA (DRIVE LANE)**
- 75mm ASPHALT
 - 100mm GRANULAR BASE
 - 250mm GRANULAR SUBBASE*
- ASPHALT PAVING AREA (WALKWAY)**
- 50mm ASPHALT
 - 150mm GRANULAR BASE*
- EX. GRAVEL PARKING LOT**
- RE-GRADE EX. 200mm DRIVEWAY CHIP GRAVEL
- NEW GRAVEL PARKING LOT**
- 200mm DRIVEWAY CHIP GRAVEL
 - 250mm GRANULAR SUBBASE*
- *PLACED ON A GEOTECHNICALLY APPROVED SUBGRADE

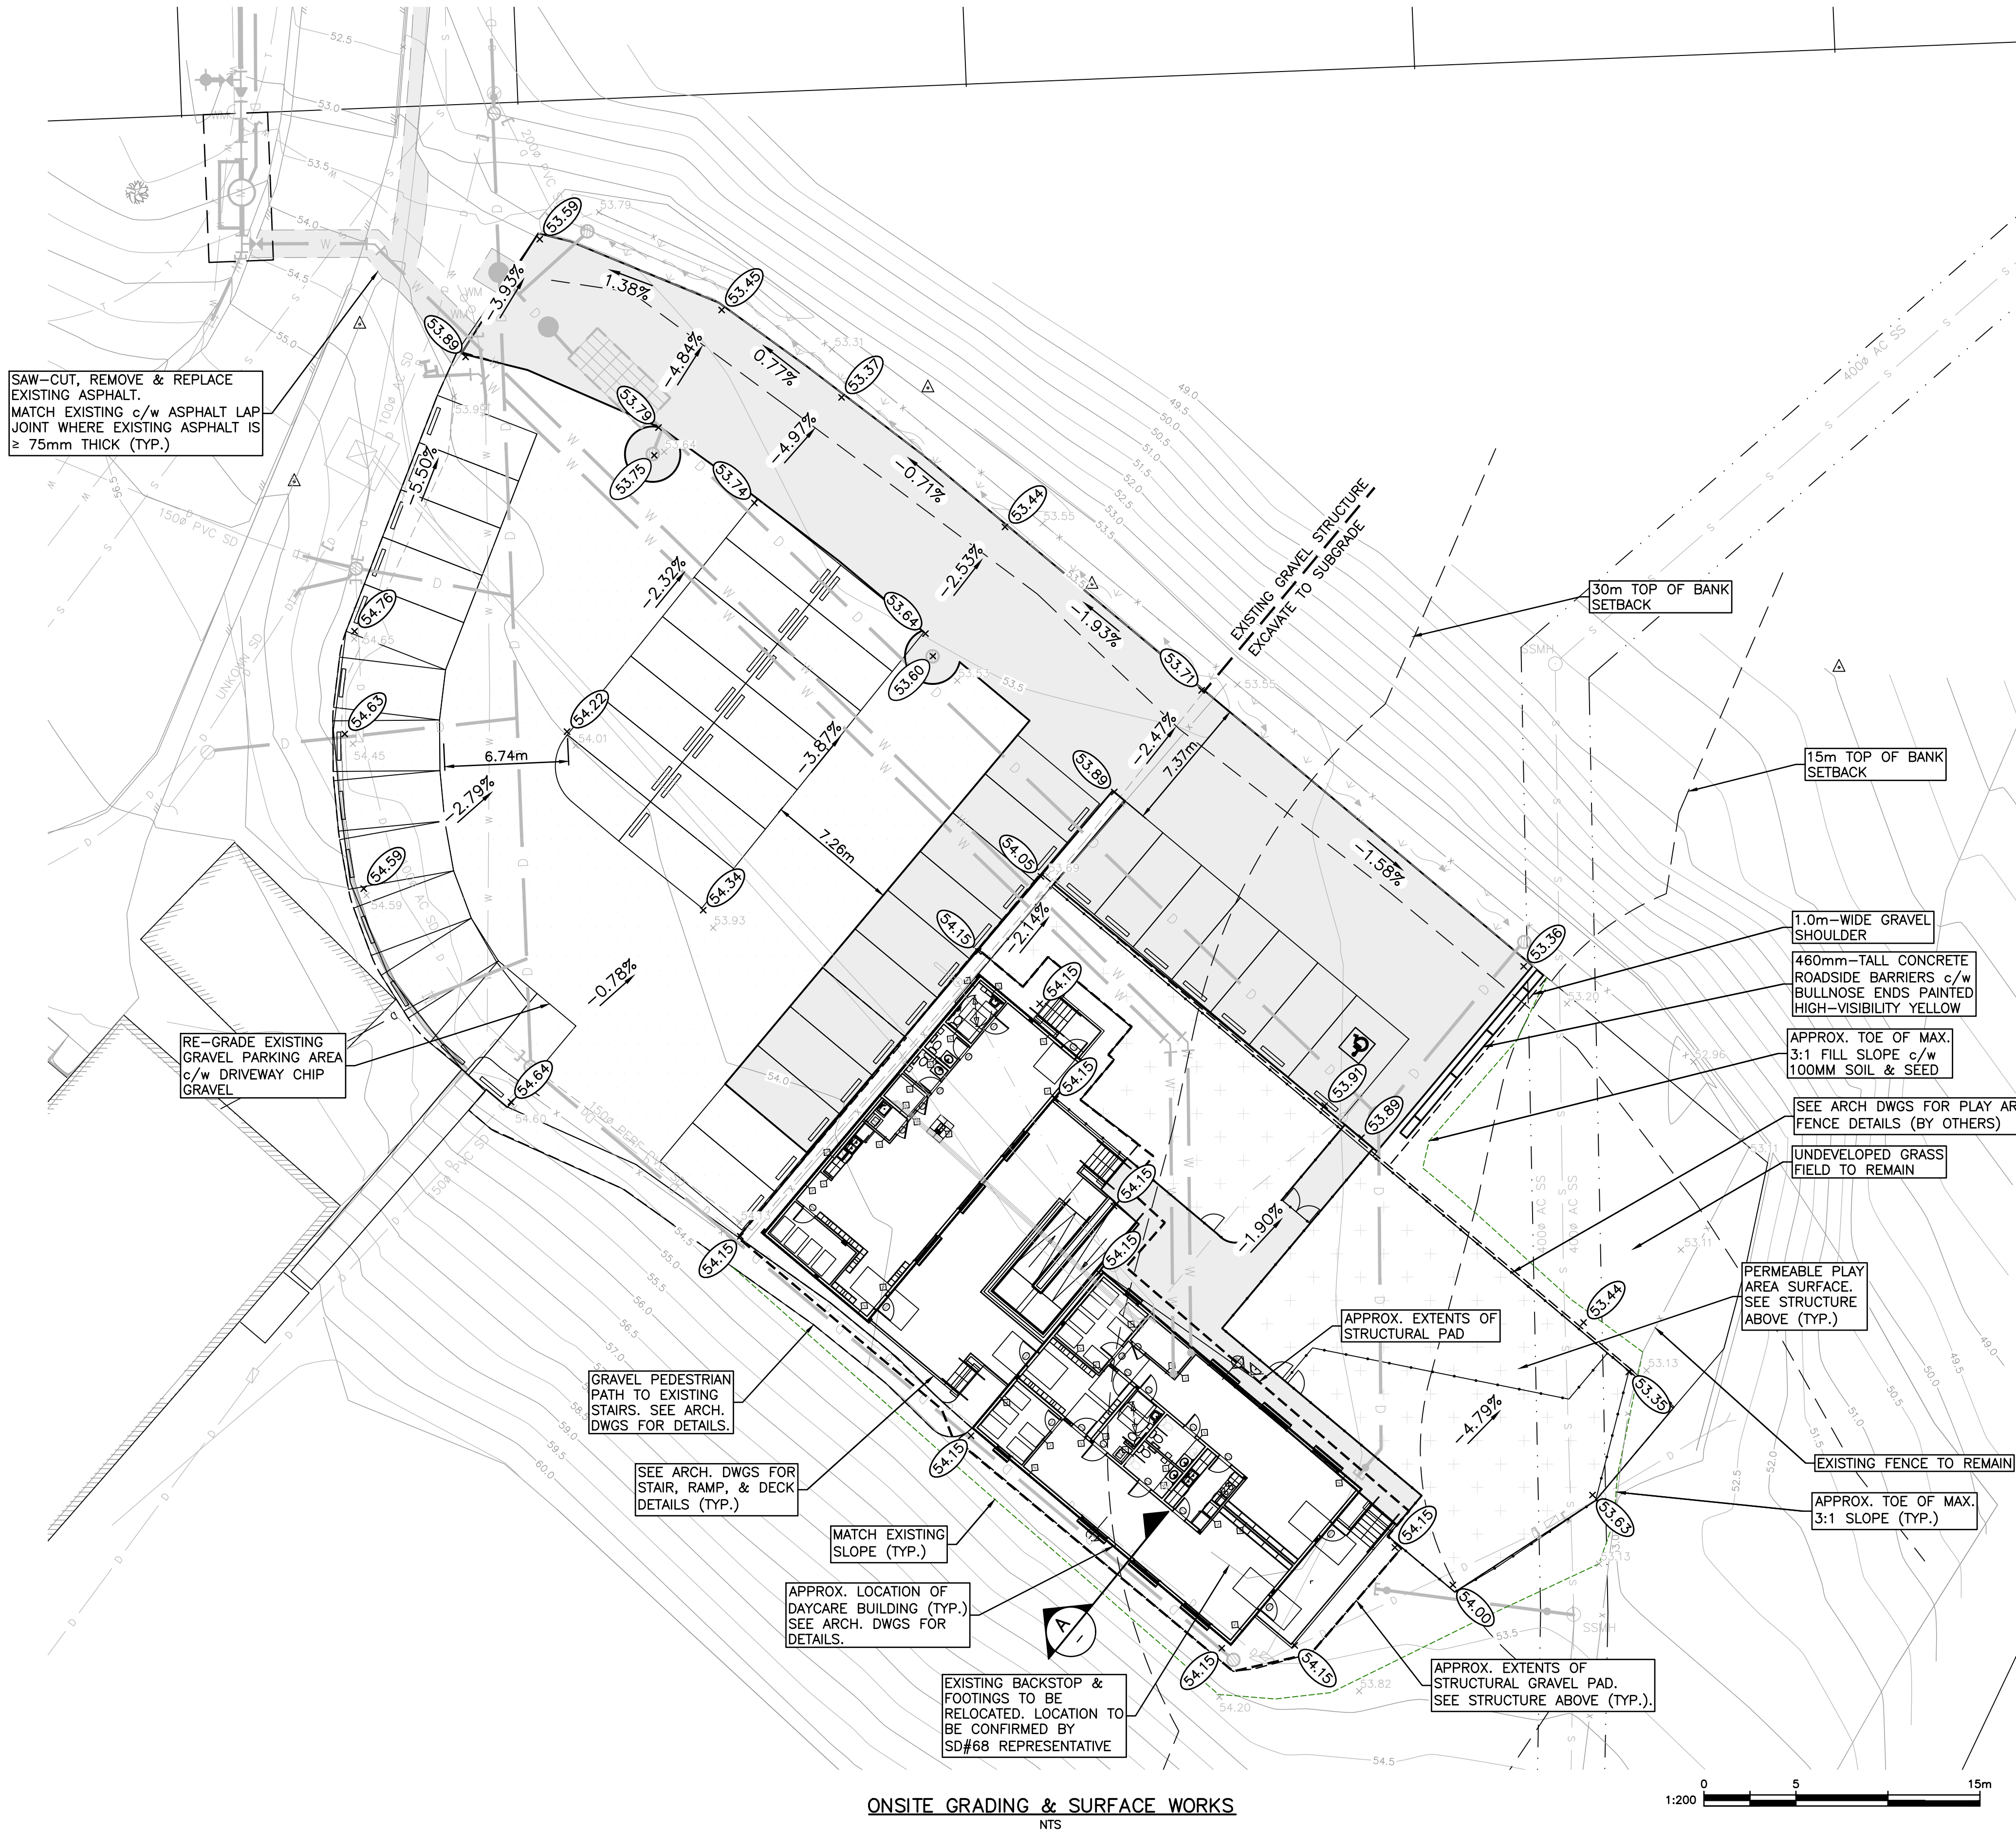


ONSITE GRADING & SURFACE WORKS
NTS

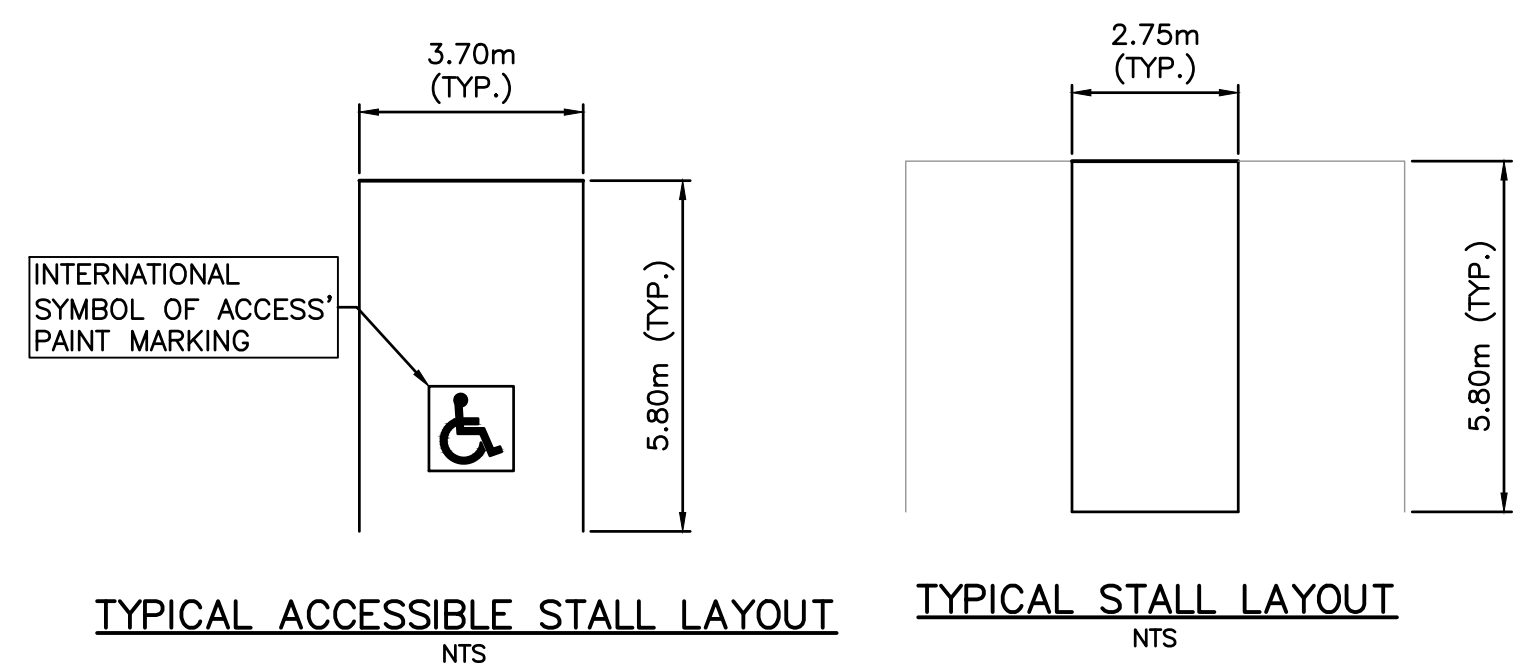


TYPICAL ACCESSIBLE STALL LAYOUT
NTS

TYPICAL STALL LAYOUT
NTS

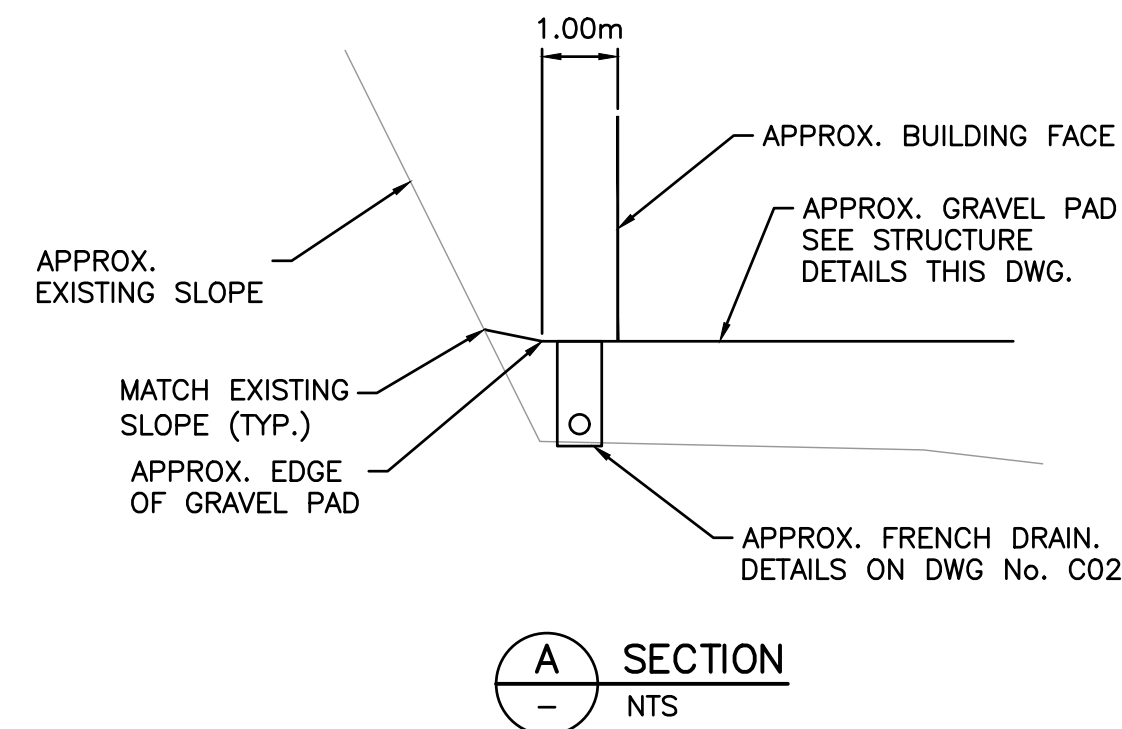

A
SECTION
NTS

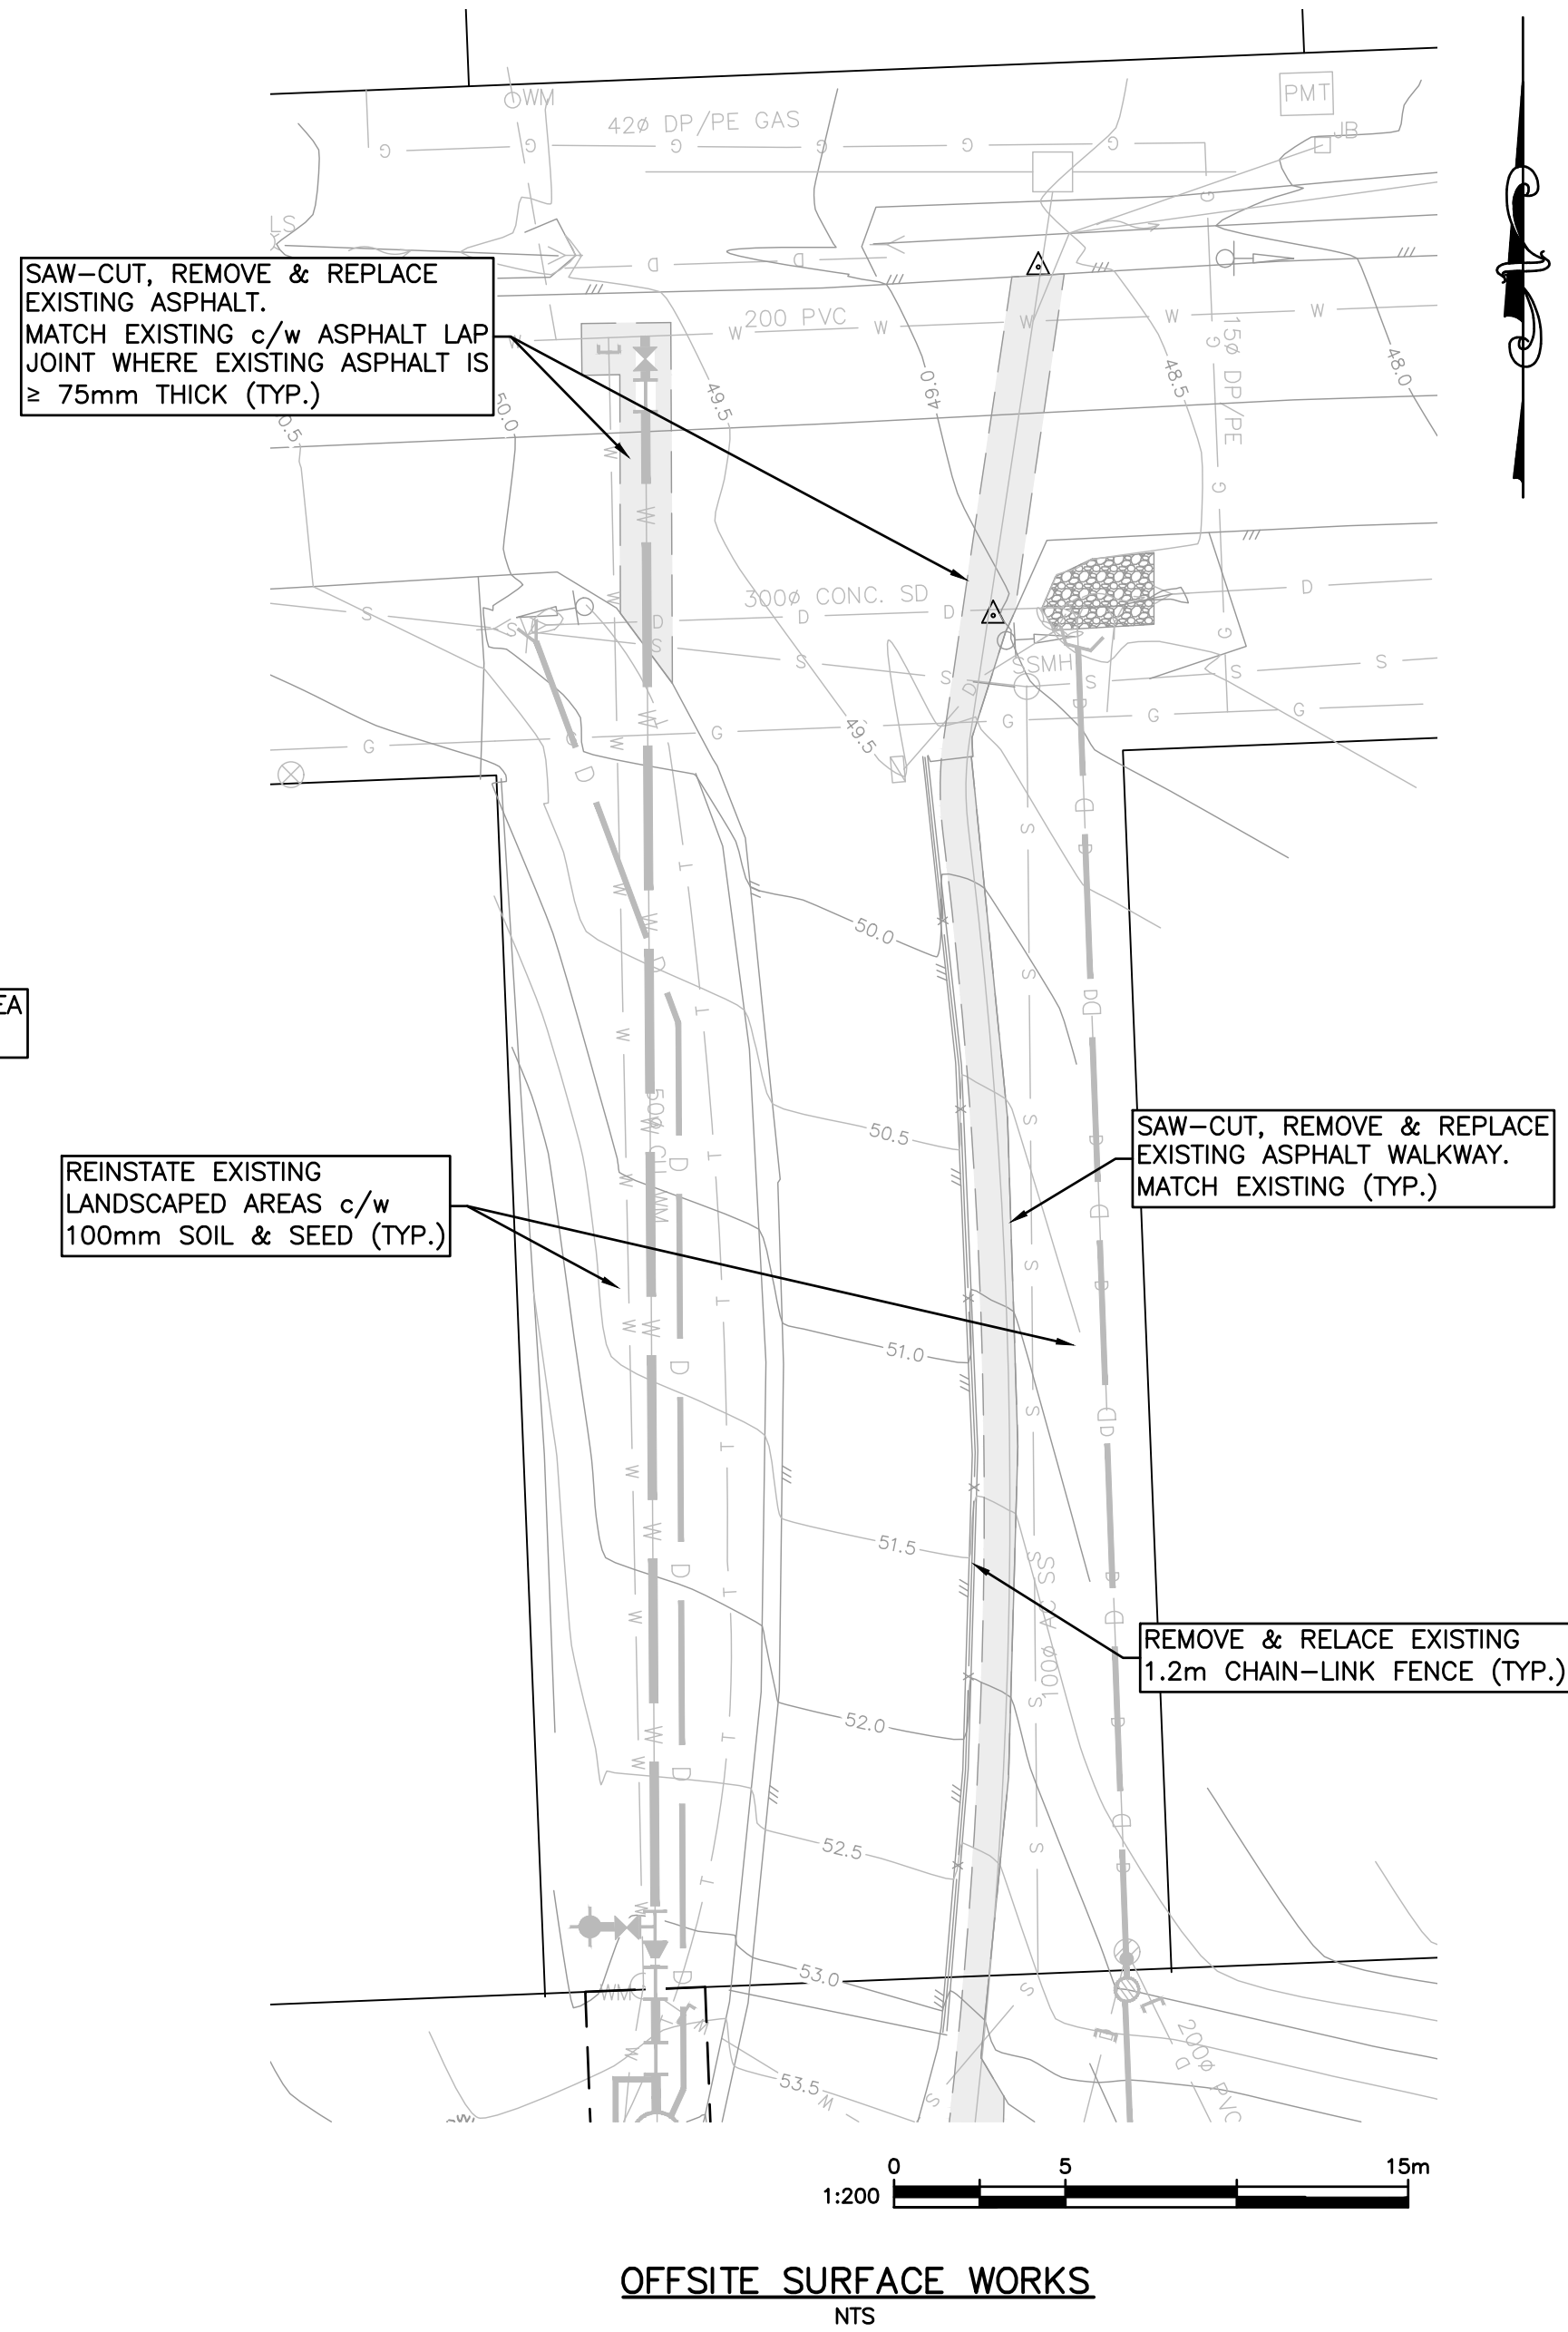

OFFSITE SURFACE WORKS
NTS

ISSUES		
No.	DATE	ISSUED FOR
A	2025.05.22	COORDINATION
B	2025.07.11	BUILDING PERMIT
C	2025.12.18	BUILDING PERMIT
D	2026.04.13	TENDER

NOT FOR
CONSTRUCTION

ISSUED FOR TENDER

CILAIRE ELEMENTARY
MODULAR DAYCARE STUDIO
SITE WORKS

25 CILAIRE DRIVE, NANAIMO, BC

SCHOOL DISTRICT 68 NANIMO/LADYSMITH


**HEROLD
ENGINEERING**
3701 Shenton Rd, Nanaimo, BC V9T 2H1
Tel: 250-751-8558 Fax: 250-751-8559
Email: mail@heroldengineering.com

SITE GRADING
& SURFACE WORKS


DESIGNED SMJ	ENGINEER'S SEAL Permit to Practice No. 1000201
DESIGN REVIEW PGR	
DRAFTED GV	
DRAFTING REVIEW PGR	
PROJECT No. 0016-352	CLIENT DRAWING No.
SCALE H: 1:200 V: N/A	PERMIT No.
HEL DRAWING No. C03	REVISION 3 OF 6 D

DESTROY ALL DRAWINGS SHOWING PREVIOUS REVISION

1. FOR GENERAL NOTES SEE DWG. No. C01

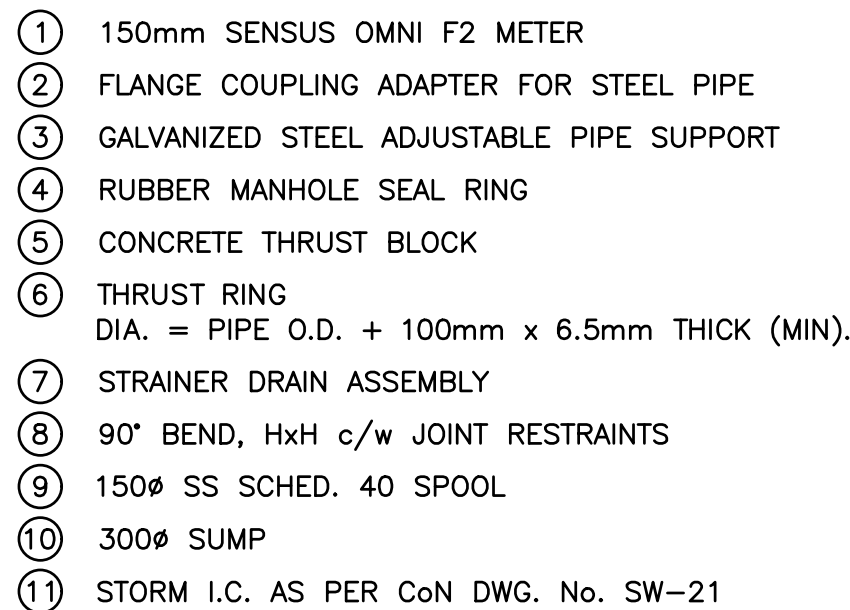

1. THRUST BLOCKING TO BE INSTALLED AS REQUIRED.
2. METER ASSEMBLY TO BE SUPPORTED BY STEEL PIPE SUPPORTS AS REQUIRED.
3. FABRICATED STAINLESS STEEL PIPE AND FITTINGS TO BE 304 SCHEDULE 40 TO AWWA C-210 & NSF-61 SPECIFICATIONS.
4. PIT MOUNT RADIO ASSEMBLY PER CoN REQUIREMENTS. CONFIRM WITH CoN REPRESENTATIVE PRIOR TO INSTALLATION.
5. ONLY PRODUCTS APPROVED BY THE CITY ENGINEER OR LISTED IN THE CITY OF NANAIMO APPROVED PRODUCTS LIST WILL BE ACCEPTED FOR INSTALLATION. ONLY UL/FM LISTED PRODUCTS SHALL BE APPROVED FOR FIRELINE SERVICE.

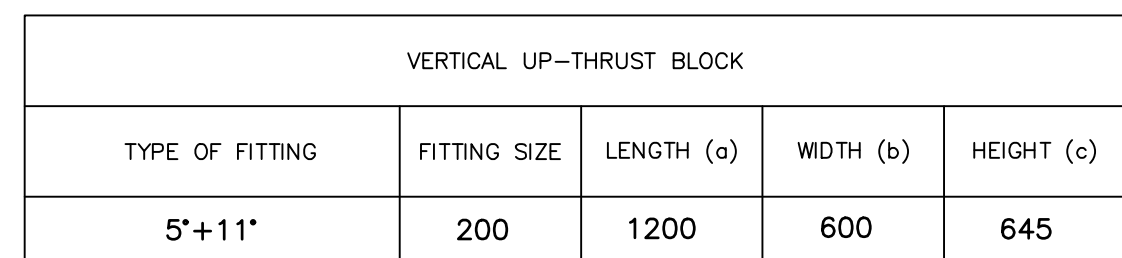

GENERAL THRUST BLOCK NOTES:

1. THRUST BLOCK FORMED ON BLASTED ROCK FILL, ROCK, OR SILT TILL.*
2. POLYETHYLENE BOND BREAKER USED BETWEEN CONCRETE AND FITTINGS.
3. ALL CONCRETE 32 MPa UNLESS OTHERWISE SHOWN.
4. ALL DIMENSION ARE IN MILLIMETERS UNLESS OTHERWISE SHOWN.
5. JOINT RESTRAINT INSTALLED AS WELL.
6. ALL BOLTS AND NUTS ARE STAINLESS STEEL.

6 MODULES @ 0.914m (5.48m)



FINAL VENT LOCATION TO BE CONFIRMED WITH SHOP DRAWINGS

200Ø PVC SDR35 OUTLET

200Ø PVC SDR35 INLET

0.457m (2.29m)

(SHOP DRAWING REQUIRED PRIOR TO CONSTRUCTION)

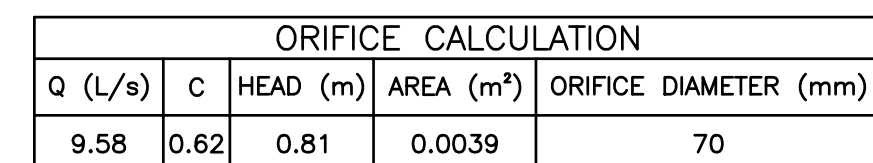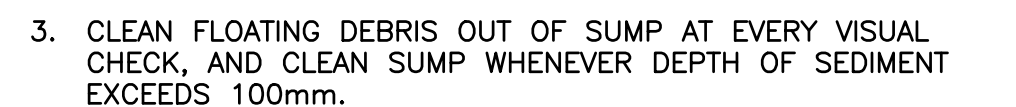

BACKFLOW PREVENTER

50a SENSUS C2 WATER METER WITH INTEGRAL FLOW STRAINER, CW RADIO READOUT 510M DUAL PORT INSTALLED ON EXTERIOR FACE OF BUILDING, TO BE USED FOR BOTH METERS. COORDINATE LOCATION OF READOUT ON SITE WITH AUTHORITY HAVING JURISDICTION.

75a

N.C.

50a

PROVIDE LOCK OUT IN DOMESTIC BY PASS

38a

50a

20a SYSTEM DRAIN VALVE

50a

PRESSURE GAUGE (TYP.)

38a DOWN TO DAYCARE: REFER TO FLOOR PLANS FOR CONTINUATION.

38a HEAT TRACED DOWN BELOW BUILDING TO BEFORE/AFTER CARE STUDIO REFER TO FLOOR PLANS FOR CONTINUATION.

FULL FLOW PRV W/ STRAINER

MECH ROOM FLOOR (DAYCARE)

CRAWLSPACE

GROUND

100a

COMBINED WATER TO BUILDING, REFER TO FLOOR PLANS FOR CONTINUATION.

THRUST BLOCK

TO SPRINKLER TREE: REFER TO SCHEMATIC 204-6

*SEE MECHANICAL DRAWINGS FOR DETAILS



(SHOP DRAWING REQUIRED PRIOR TO CONSTRUCTION)

*DETAIL TO BE READ IN CONJUNCTION WITH CoN STD. DWG. Nos. W-11A & W-13


NOT FOR
CONSTRUCTION

ISSUED FOR TENDER

CILAIRE ELEMENTARY
MODULAR DAYCARE STUDIO
SITE WORKS

225 CILAIRE DRIVE, NANAIMO, BC

SCHOOL DISTRICT 68 NANIMO/LADYSMITH

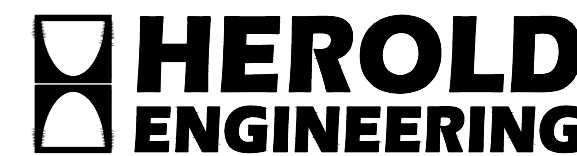


3701 Shenton Rd, Nanaimo, BC V9T 2H1
Tel: 250-751-8558 Fax: 250-751-8559
Email: mail@heroldengineering.com

©Copyright reserved. This drawing remains the exclusive property of Herold Engineering Limited and may not be reused or reproduced without written consent of Herold Engineering Limited.

DETAILS

DESIGNED SMJ	ENGINEER'S SEAL Permit to Practice No. 1000201
DESIGN REVIEW PGR	
DRAFTED GV	
DRAFTING REVIEW PGR	
PROJECT No. 0016-352	CLIENT DRAWING No.
SCALE H: 1/4" V: 1/4"	PERMIT No.
HEL DRAWING No. C04	
4 OF 6	REVISION D

File: H:\Projects\0016-352 Cilaire - Modular Daycare Studio\Civil\04C Drawings.dwg Plot Time: Apr. 10, 26 4:52 PM User: Scott Jensen

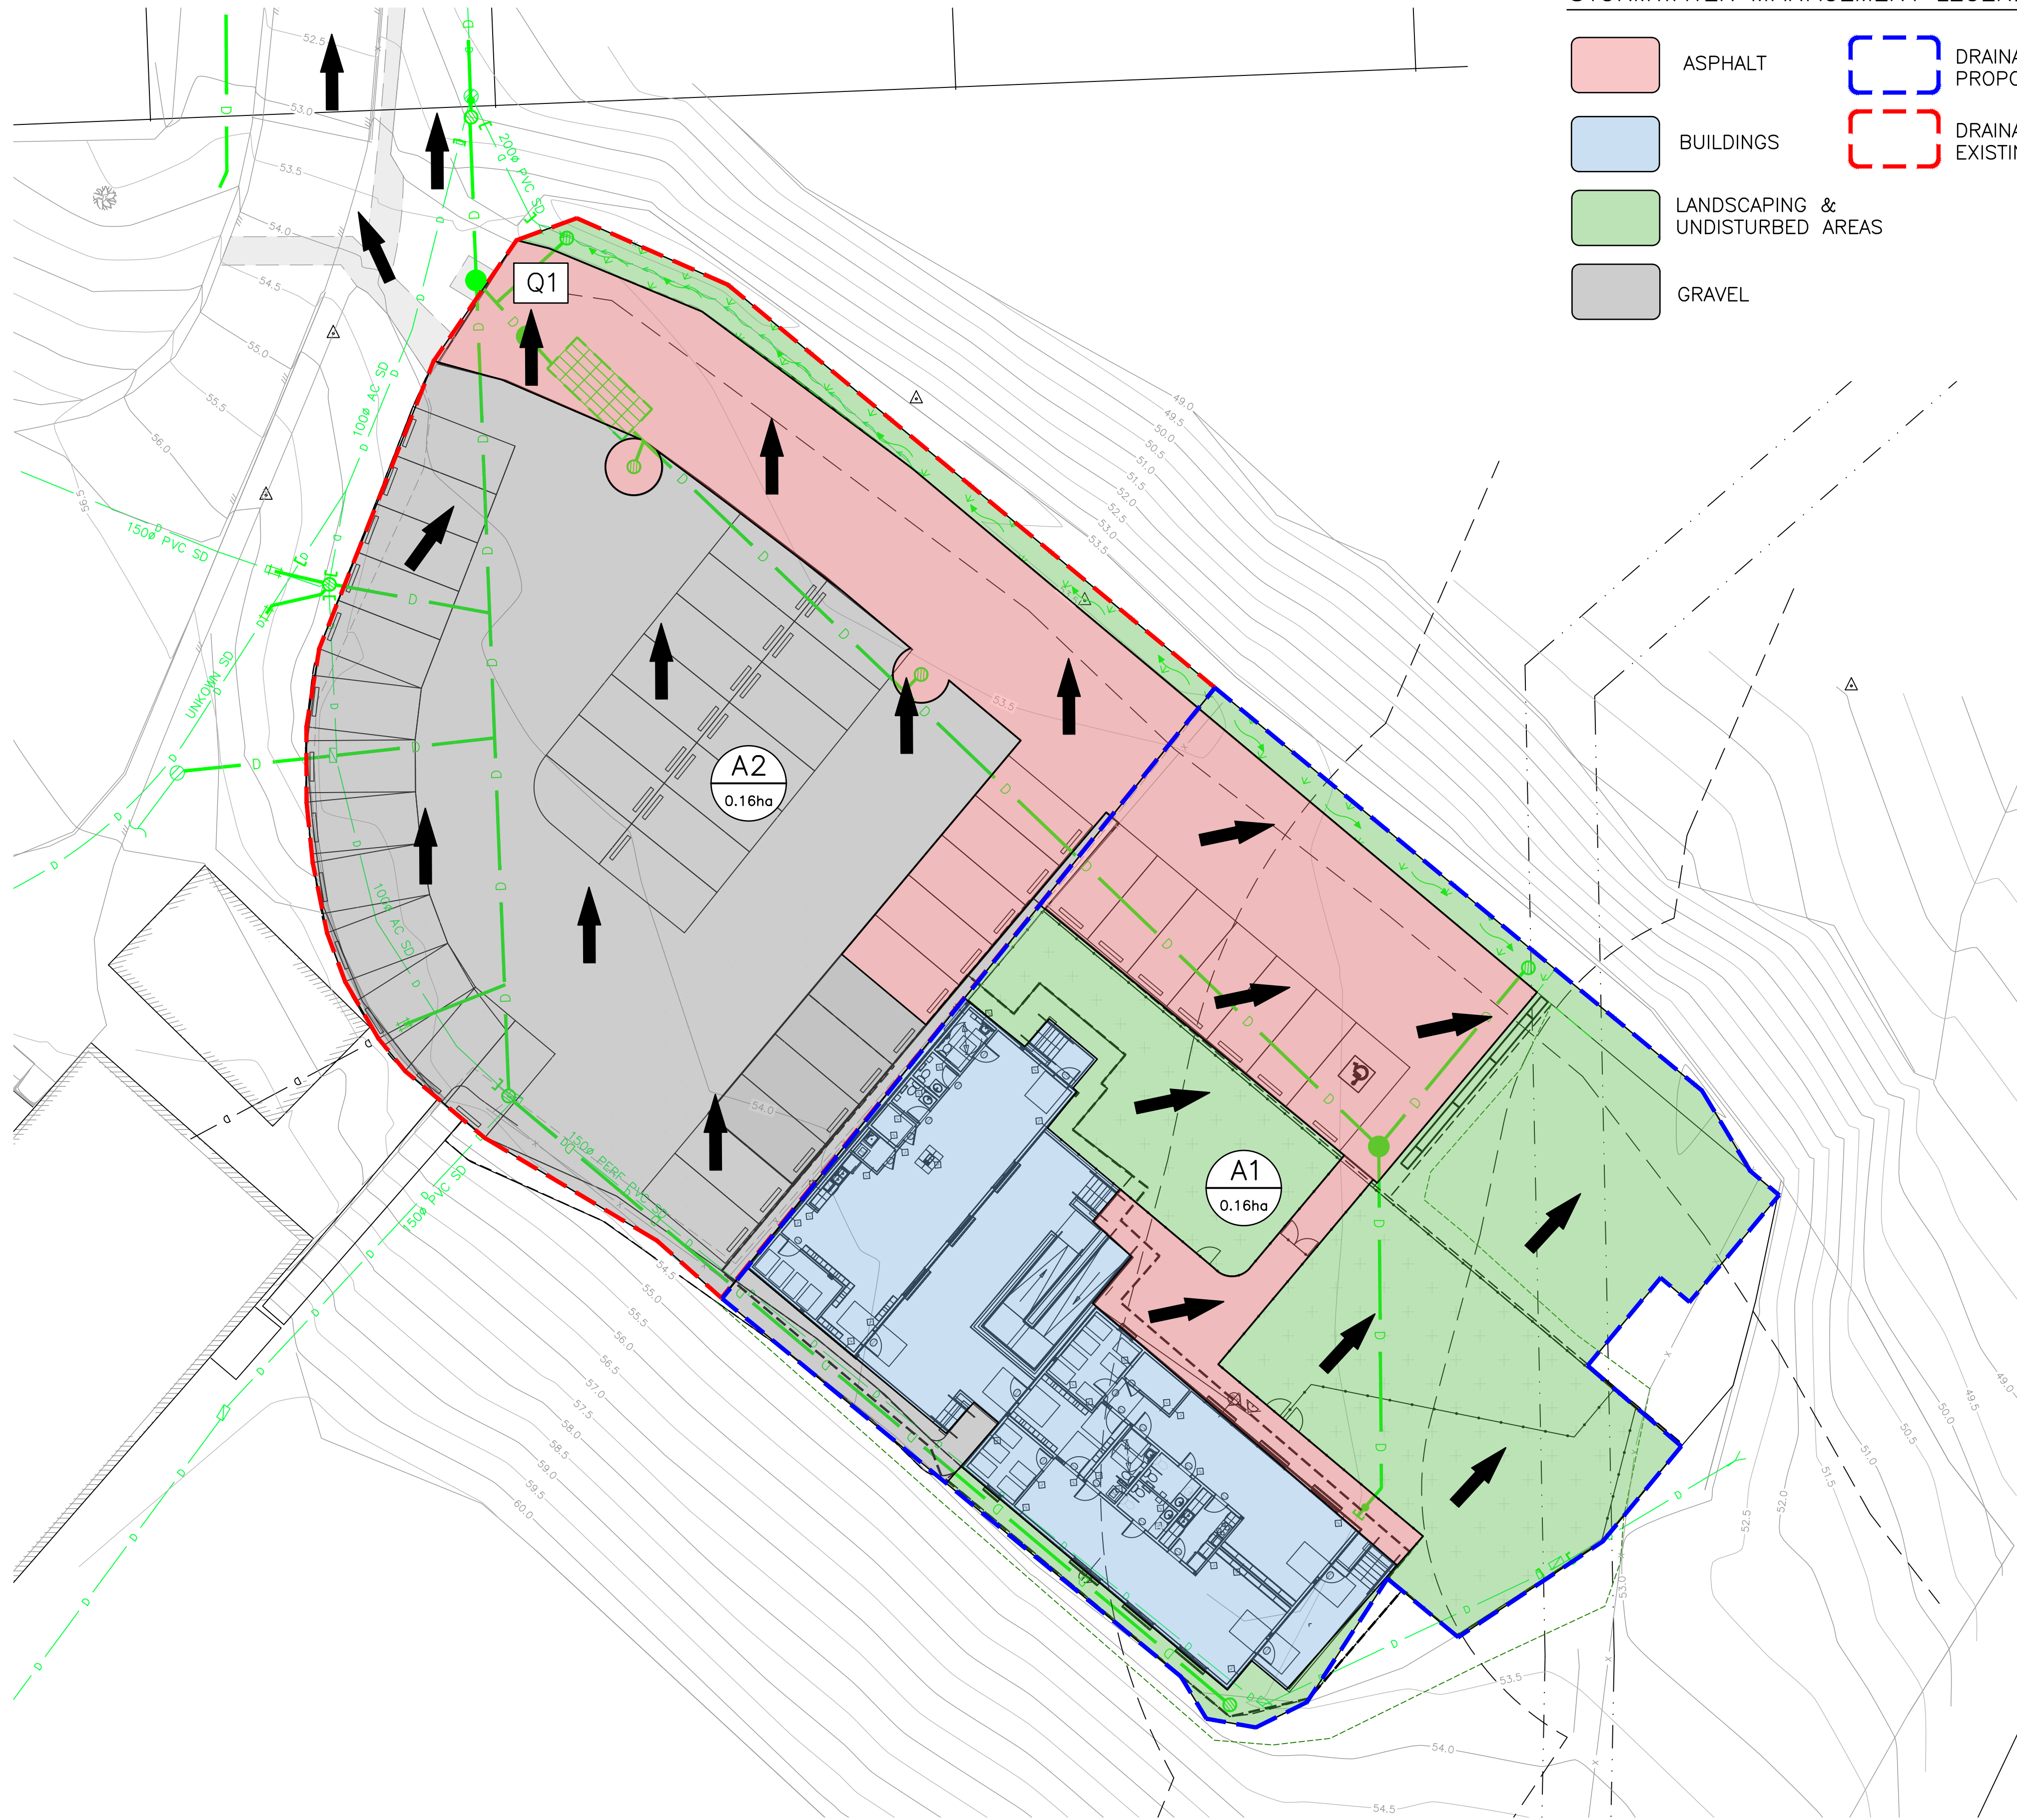

STORMWATER MANAGEMENT LEGEND

- ASPHALT
- BUILDINGS
- LANDSCAPING & UNDISTURBED AREAS
- GRAVEL
- DRAINAGE CATCHMENT AREA A: PROPOSED DAYCARE
- DRAINAGE CATCHMENT AREA B: EXISTING PARKING LOT

A1 CATCHMENT AREA
xxx ha

MAJOR STORM EVENT ROUTING (OVERLAND) 100 YEAR

Q1 5yr= 26.1 L/s
100yr= 128.8 L/s

NOTES:
1. FOR GENERAL NOTES SEE DWG. No. C01.

ISSUES		
No.	DATE	ISSUED FOR
A	2025.05.22	COORDINATION
B	2025.07.11	BUILDING PERMIT
C	2025.12.18	BUILDING PERMIT
D	2026.04.13	TENDER

NOT FOR CONSTRUCTION

ISSUED FOR TENDER

CILAIRE ELEMENTARY
MODULAR DAYCARE STUDIO
SITE WORKS



25 CILAIRE DRIVE, NANAIMO, BC
SCHOOL DISTRICT 68 NANIMO/LADYSMITH

HEROLD ENGINEERING
3701 Shenton Rd, Nanaimo, BC V9T 2H1
Tel: 250-751-8558 Fax: 250-751-8559
Email: mail@heroldengineering.com

©Copyright reserved. This drawing remains the exclusive property of Herold Engineering Limited and may not be reused or reproduced without written consent of Herold Engineering Limited.


STORMWATER MANAGEMENT PLAN	
DESIGNED SMJ	ENGINEER'S SEAL Permit to Practice No. 1000201
DESIGN REVIEW PGR	
DRAFTED GV	
DRAFTING REVIEW PGR	
PROJECT No. 0016-352	CLIENT DRAWING No.
SCALE H: 1:200 V: N/A	PERMIT No.
HEL DRAWING No. C05	REVISION D

File: H:\Projects\0016-352 Cilaire - Modular Daycare Studios\Civil\04C Drawings.dwg Plot Time: Apr. 10, 26 4:52 PM User: Scott Jensen

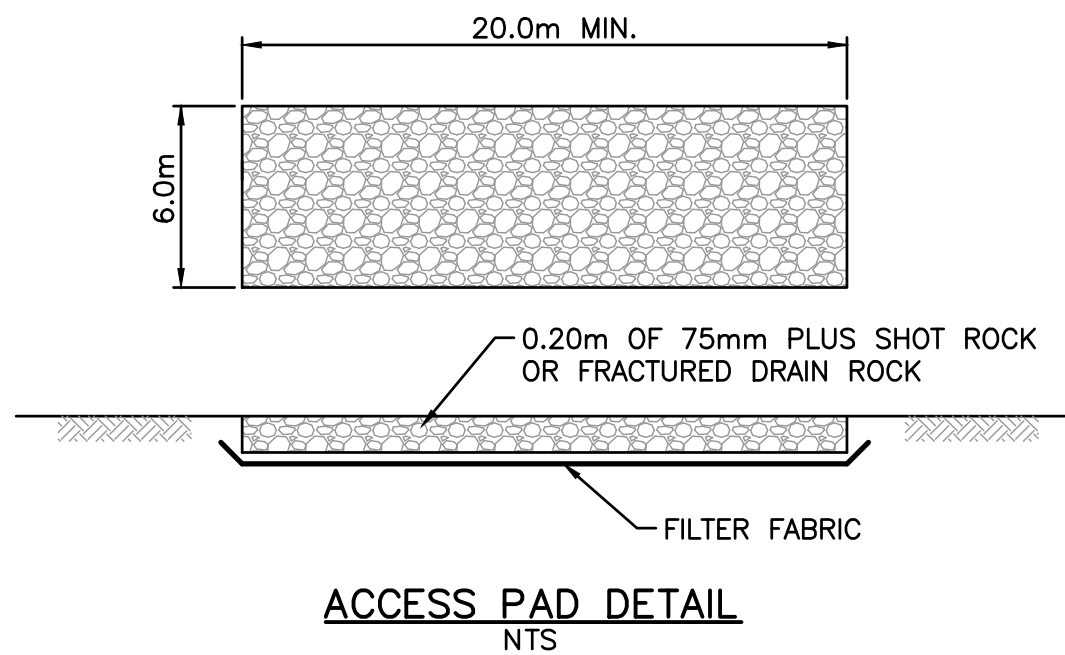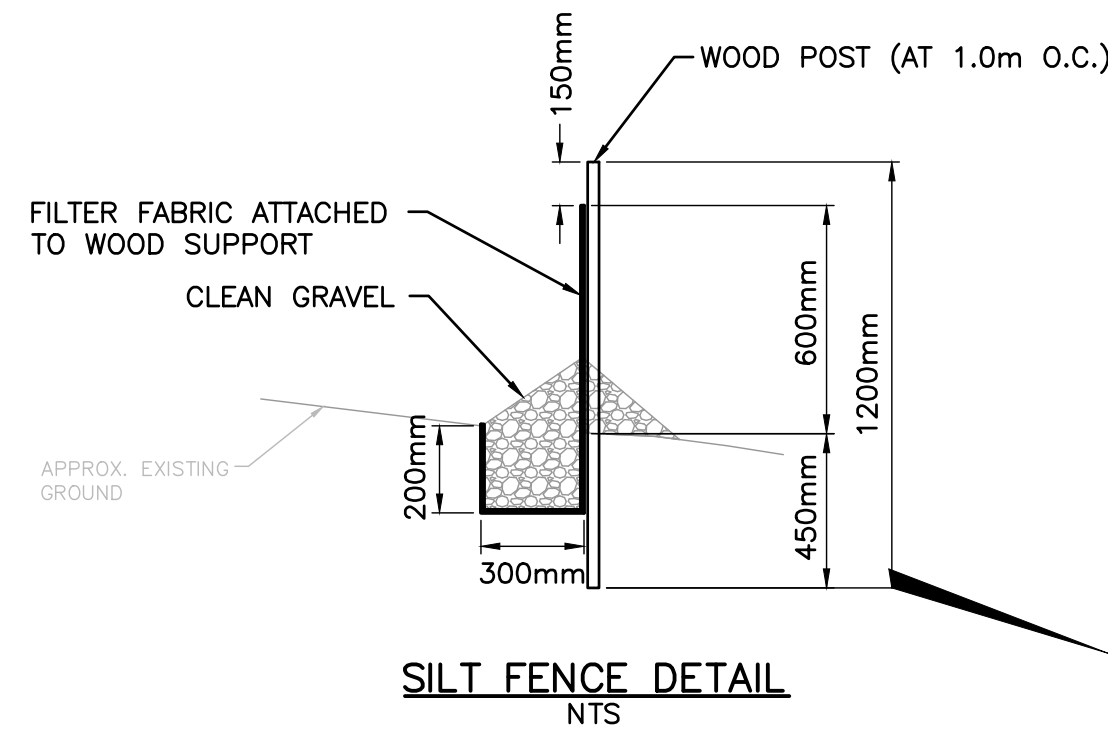

LEGEND

- OVERLAND FLOW
- TEMPORARY SILT FENCE

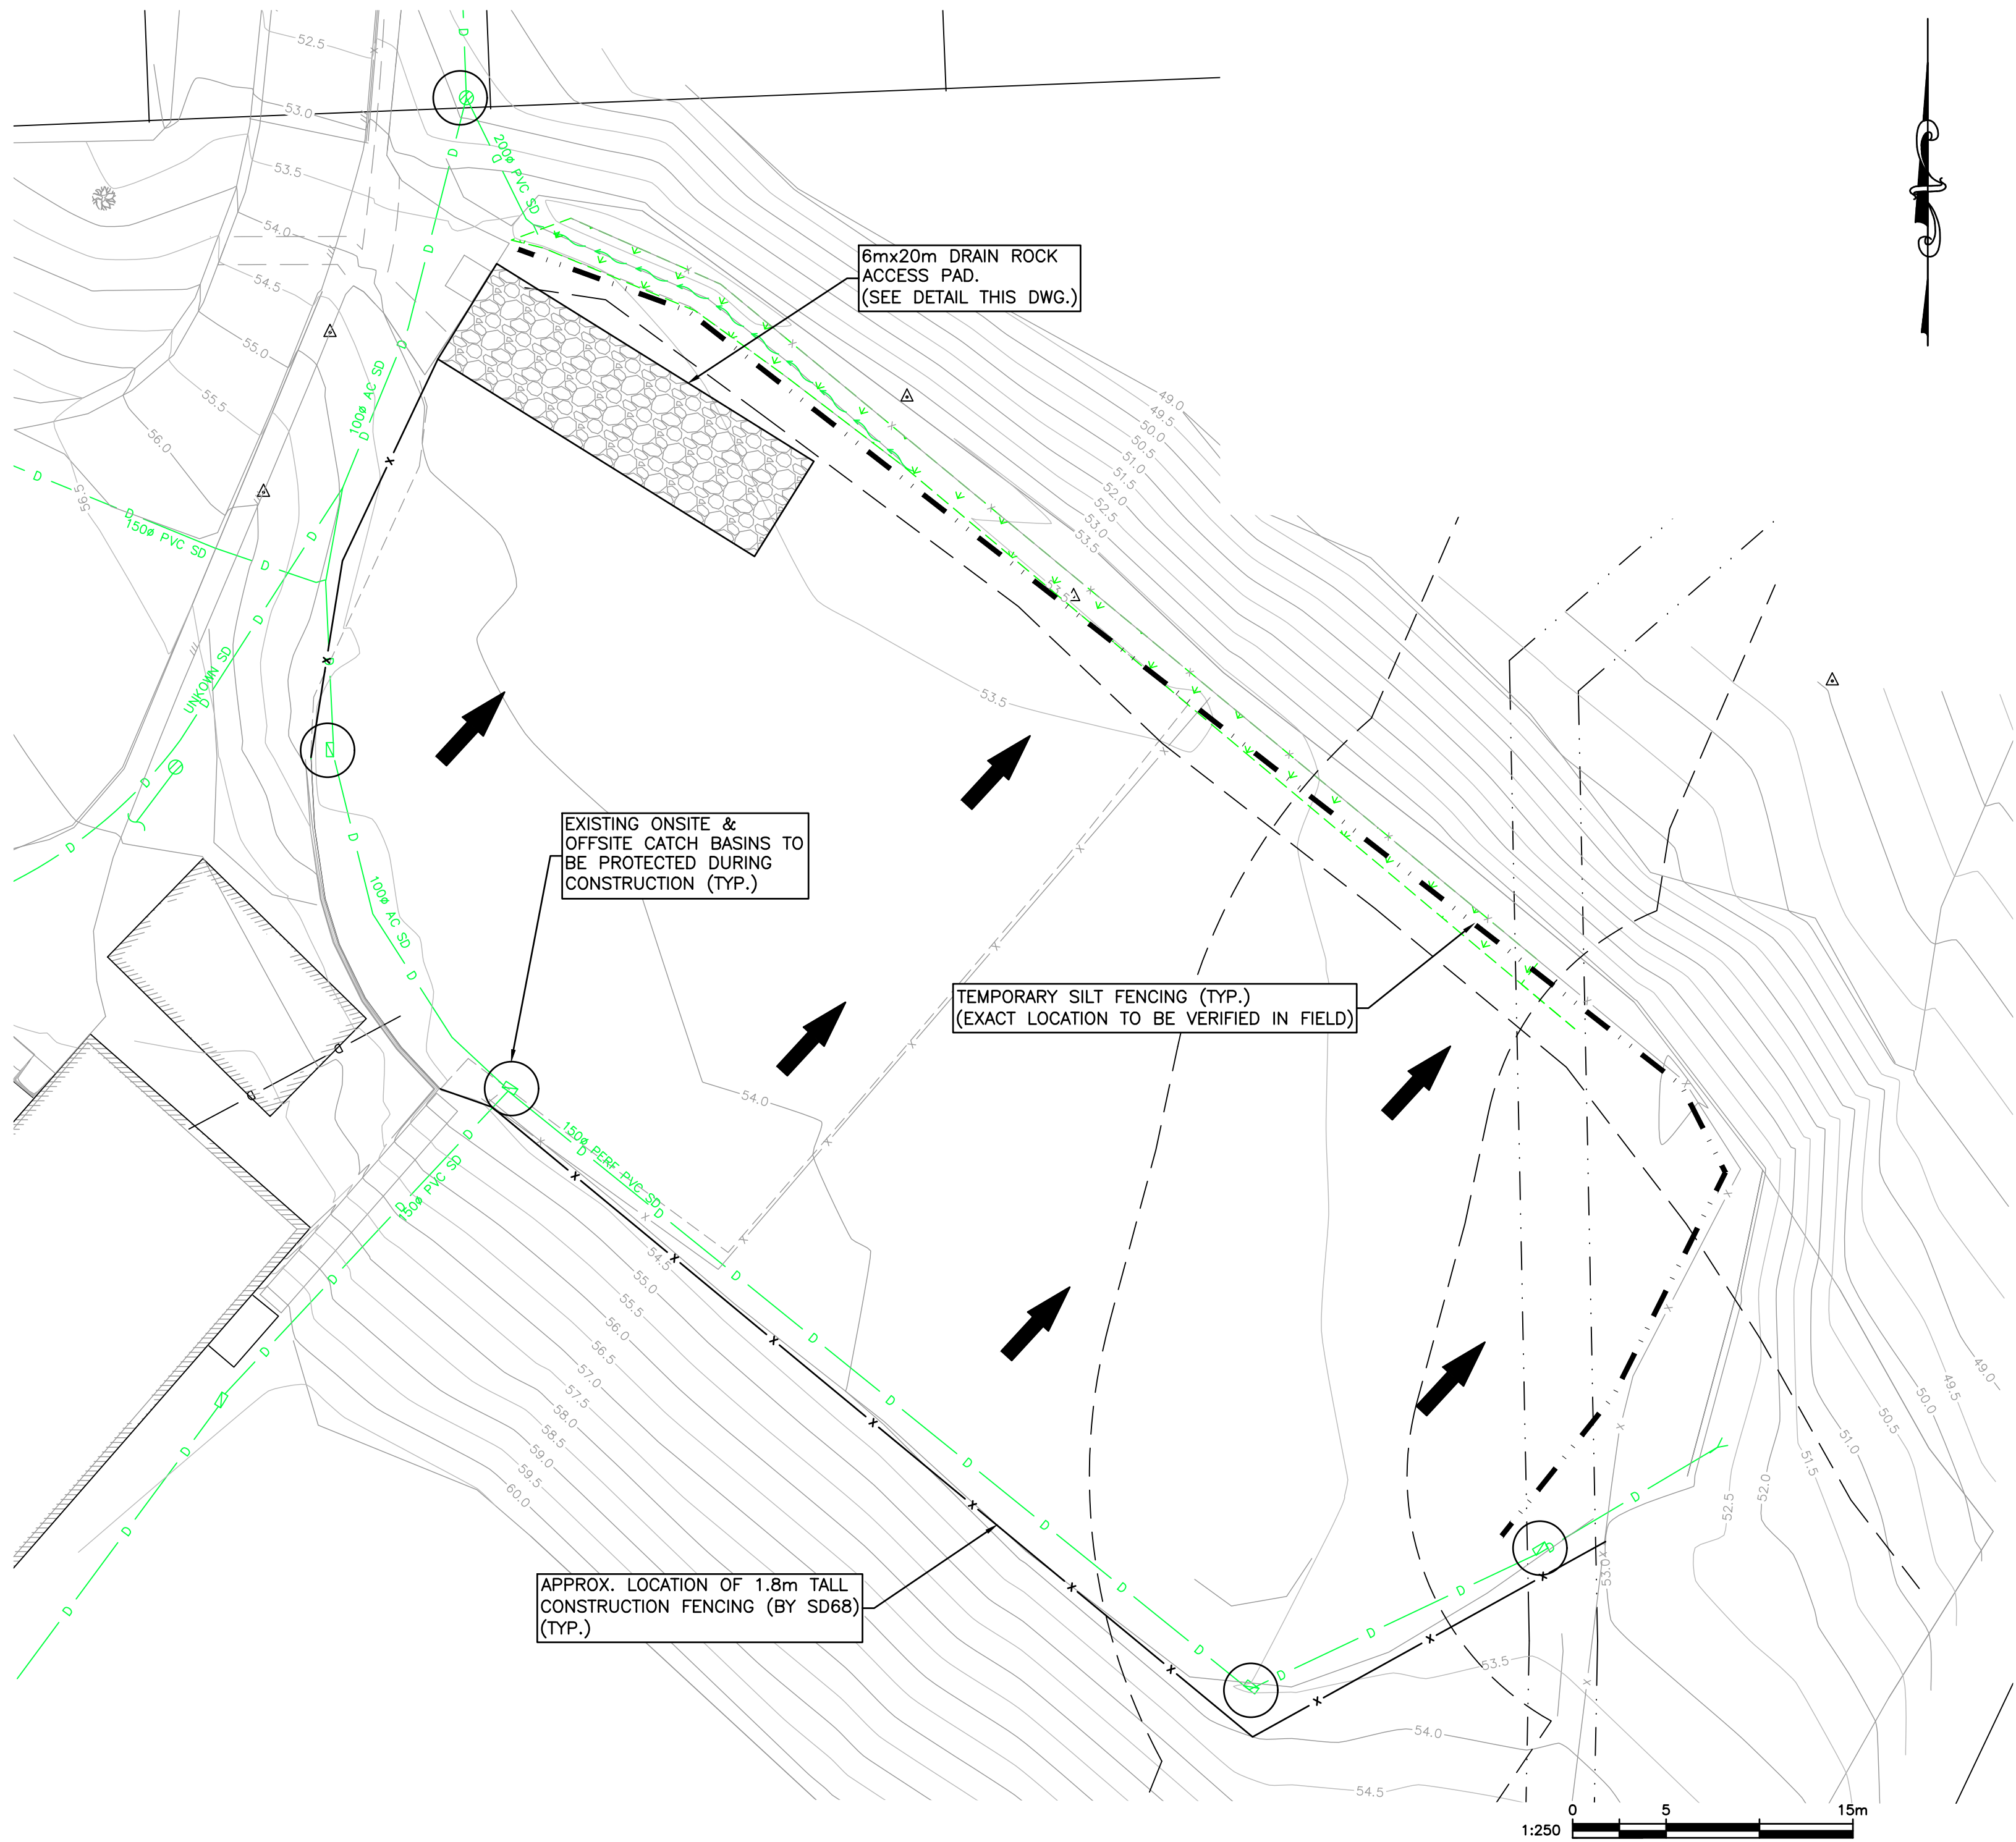

EROSION & SEDIMENT CONTROL NOTES:

1. EROSION AND SEDIMENT CONTROL FOR THIS PROJECT WILL BE AS OUTLINED IN THE FISHERIES AND OCEANS CANADA & MINISTRY OF WATER, LANDS AND AIR PROTECTION HANDBOOK ENTITLED "LAND DEVELOPMENT GUIDELINES FOR THE PROTECTION OF THE AQUATIC HABITAT, SEPTEMBER 1993" AND "ENVIRONMENTAL BEST MANAGEMENT PRACTICES FOR URBAN AND RURAL LAND DEVELOPMENT IN BRITISH COLUMBIA, JUNE 2004" AND "EROSION & SEDIMENT CONTROL GUIDELINE" BY THE CITY OF NANAIMO. IT IS INCUMBENT UPON THE CONTRACTOR TO ACQUIRE THESE GUIDELINES AND FAMILIARIZE HIMSELF WITH THE REQUIREMENTS WITHIN.
2. THE CONSULTANT ASSUMES NO RESPONSIBILITY FOR DAMAGES RESULTING FROM IMPROPER EROSION AND SEDIMENT CONTROL MEASURES UNDERTAKEN BY THE CONTRACTOR.
3. ANY DIRECTION GIVEN BY THE CONSULTANT OR CITY TO THE CONTRACTOR FOR EROSION AND SEDIMENT CONTROL AND NOT FOLLOWED BY THE CONTRACTOR IS TO BE REPORTED TO THE CITY IMMEDIATELY.
4. THIS ESC PLAN IS INTENDED TO PROVIDE A GENERAL OVERVIEW OF BEST MANAGEMENT PRACTICES TO BE IMPLEMENTED ONSITE. CONTRACTOR IS RESPONSIBLE FOR PROPER ESC PLAN IMPLEMENTATION AND IS TO UPDATE AND PROVIDE STAGED ESC PLANS TO SUIT CONSTRUCTION PHASES AS NEEDED.
5. ROUTINE INSPECTION AND MAINTENANCE OF THE SYSTEM COMPONENTS WILL BE THE RESPONSIBILITY OF THE CONTRACTOR. THE CONTRACTOR SHOULD DESIGNATE A QUALIFIED ON-SITE PERSON TO BE RESPONSIBLE FOR DAY-TO-DAY MANAGEMENT AND MONITORING OF THE ESC PLAN. AT A MINIMUM, INSPECT AND DOCUMENT ALL BMP'S WEEKLY AND AFTER PRECIPITATION EVENTS TO ENSURE PROPER FUNCTION.
6. DEFICIENCIES DOCUMENTED DURING INSPECTION OF ESC MEASURES MUST BE CORRECTED PROMPTLY, AND MAINTENANCE DOCUMENTED.
7. INSPECTION REPORTS AND ESC PLAN MUST BE KEPT ON SITE AT ALL TIMES. ENGINEER OR GOVERNING AUTHORITY MAY REQUEST A COPY OF INSPECTION DOCUMENTS AT ANY TIME. COPIES OF INSPECTION REPORTS ARE TO BE PROVIDED UPON REQUEST.
8. IT IS THE RESPONSIBILITY OF THE CONTRACTOR TO ENSURE NO MUD, DIRT, SOIL, SILT OR ANY OTHER SUBSTANCES ARE SPILLED, DROPPED, WASHED OR TRACKED ONTO PUBLIC RIGHTS OF WAY, OR AREAS THAT LEAD TO CATCH BASINS CONNECTED TO PUBLIC SYSTEMS. THE CONTRACTOR IS TO CLEAN ANY SUCH MATERIAL IMMEDIATELY. I.E. STREETS ARE TO BE SWEEP WITH A VACUUM STREET SWEEPER AFTER WORK STOPPAGE EACH DAY.
9. PRIOR TO CONSTRUCTION, INSTALL A TEMPORARY GRAVEL CONSTRUCTION ENTRANCE/EXIT TO LIMIT TRACKING OF SITE SOILS ONTO OFFSITE ROADWAYS. THE WIDTH OF THE PAD SHOULD NOT BE LESS THAN THE FULL WIDTH OF POINT OF INGRESS OR EGRESS IN ANY CASE SHOULD NOT BE LESS THAN 6m WIDE WITH A LENGTH OF THE PAD NOT LESS THAN 20m AND HAVING A MINIMUM THICKNESS OF 200mm (8") OF COARSE GRANULAR MATERIAL. COARSE GRANULAR MATERIAL SUCH AS 75mm PLUS SHOT ROCK OR FRACTURED DRAIN ROCK UNDERLAIN WITH GEO-TEXTILE FABRIC IS RECOMMENDED.
10. THE ENTRANCE SHOULD BE MAINTAINED FOR THE DURATION OF CONSTRUCTION, IN A CONDITION THAT WILL PREVENT TRACKING OF SEDIMENT ONTO PUBLIC RIGHT OF WAYS, OR AREAS THAT LEAD TO CATCH BASINS CONNECTED TO PUBLIC SYSTEMS. THIS MAY REQUIRE PERIODIC TOP DRESSING WITH ADDITIONAL MATERIAL AS CONDITIONS DEMAND. THE PAD MAY BE REMOVED ONCE PERMANENT PAVEMENTS ARE IN PLACE AT THE SITE. A WHEEL WASH MAY BE REQUIRED IF THE TEMPORARY GRAVEL PAD IS NOT ADEQUATELY FUNCTIONING.
11. PRIOR TO CONSTRUCTION, CONTRACTOR TO CLEARLY FLAG OR FENCE AREAS OF NO DISTURBANCE AS WELL AS ANY DESIGNATED TREES AND SHRUBS THAT ARE TO BE PRESERVED. MARKINGS SHALL REMAIN IN PLACE THROUGHOUT CONSTRUCTION.
12. CONTRACTOR TO STRIP AND GRUB ONLY THOSE AREAS NECESSARY FOR THE CURRENT CONSTRUCTION. STAGE CONSTRUCTION OPERATIONS TO LIMIT DISTURBANCE AND DO NOT STRIP ANY AREA UNTIL REQUIRED.
13. DUST CONTROL MUST BE IMPLEMENTED ON THE PROJECT SITE, AS REQUIRED. WATER TRUCK MAY BE REQUIRED ONSITE OR IN CLOSE PROXIMITY DURING CONSTRUCTION. CONSTRUCTION SHALL BE HALTED DURING EXTREME WIND CONDITIONS.
14. GRADE WORK AREAS AWAY FROM ADJACENT PROPERTIES AND TOWARDS THE SEDIMENT PONDS ON SITE. EXACT LOCATION OF SEDIMENT PONDS TO BE VERIFIED IN THE FIELD.
15. INSTALL DOWN-GRADIENT PERIMETER PROTECTION (SUCH AS SILT FENCE, GRAVEL FILTER BERMS, V-DITCHES ETC) TO PROTECT OFFSITE AREAS FROM STORMWATER RUNOFF AND SEDIMENTATION DURING CONSTRUCTION. PROTECTION SHALL NOT BE REMOVED UNTIL VEGETATION/PAVEMENT IS ESTABLISHED.
16. IF GRADED AREAS WITHIN THE PROJECT WILL NOT BE COMPLETED OUTSIDE OF THE WET SEASON (OCTOBER TO APRIL), REVEGETATION OPERATIONS SHOULD BE CARRIED OUT WITHIN ONE WEEK OF GRADING COMPLETION OR NO LATER THAN SEPT. 15th.
17. ENSURE PROPER PLACEMENT AND PROTECTION OF STOCKPILED SOILS AND MATERIALS. PLACEMENT OF MATERIALS ON A STREET OR WHERE WIND/WATER COULD TRANSPORT MATERIAL OFFSITE IS PROHIBITED. ALL STOCK/SPOIL PILES TO BE COVERED WITH STRAW MULCH OR TARP TO PREVENT EROSION (HAY NOT ACCEPTABLE).
18. SEDIMENT CAPTURED BY SILT FENCES OR OTHER DEVICES SHALL BE REMOVED AND DISPOSED OF WHEN 1/3 HEIGHT OF THE DEVICE IS REACHED. AT MINIMUM, THE CONTRACTOR SHALL MONITOR AND PUMP OUT SEDIMENTATION PONDS EVERY 7 DAYS AND AFTER PRECIPITATION. PUMP HOSE SHALL BE EQUIPPED WITH SEDIMENT FILTER NOZZLE OR APPROVED ALTERNATIVE ESC PROTECTION MEASURE.
19. 48 HOURS PRIOR TO ANY PREDICTED SIGNIFICANT STORM EVENT, THE DESIGNATED SITE PERSON SHOULD INSPECT THE E&SC WORKS AND ENSURE THAT THE WORKS ARE ADEQUATE TO PROTECT THE SITE DURING THE STORM EVENT AND PROVIDE A WRITTEN REPORT TO THE ENGINEER AND/OR THE CITY UPON REQUEST. IF THE DESIGNATED SITE PERSON DETERMINES THAT THE E&SC WORKS ARE NOT ADEQUATE TO PROTECT THE SITE DURING THE ANTICIPATED STORM EVENT, THEN HE/SHE IS TO IMMEDIATELY INFORM THE ENGINEER AND CONTRACTOR SO THAT THE WORKS CAN BE MODIFIED TO ADEQUATELY PROTECT THE SITE DURING THE STORM EVENT AND PROVIDE A WRITTEN REPORT TO THE ENGINEER AND/OR THE CITY UPON REQUEST.
20. DURING AND/OR FOLLOWING EACH SIGNIFICANT STORM EVENT, THE DESIGNATED SITE PERSON SHOULD OBSERVE THE STORM DRAIN TO CONFIRM THAT TURBID WATERS FROM SOURCES ASSOCIATED WITH CONSTRUCTION ARE NOT ENTERING THE STORM DRAINAGE SYSTEM. TAKE IMMEDIATE CORRECTIVE ACTION IF INSPECTION INDICATES A PROBLEM. RECORD INSPECTION DATES, ANY SIGNIFICANT OBSERVATIONS, AND ACTIONS TAKEN, THEN INFORM THE CONSULTANT IN CHARGE AND THE APPROVING AUTHORITY.
21. THE CONTRACTOR SHALL REMOVE ALL SEDIMENT, MUD AND CONSTRUCTION DEBRIS THAT MAY ACCUMULATE IN THE FLOW LINES, PRIVATE PROPERTY AND PUBLIC RIGHTS OF WAY AS A RESULT OF THIS CONSTRUCTION PROJECT. REMOVAL SHALL BE CONDUCTED AS SOON AS POSSIBLE.
22. CITY OF NANAIMO STANDARD EROSION & SEDIMENT CONTROL SIGNAGE IS REQUIRED TO BE PLACED ON-SITE PRIOR TO THE START OF CONSTRUCTION AND MAINTAINED IN PLACE UNTIL LANDSCAPING IS COMPLETED.

ISSUES		
No.	DATE	ISSUED FOR
A	2025.05.22	COORDINATION
B	2025.07.11	BUILDING PERMIT
C	2025.12.18	BUILDING PERMIT
D	2026.04.13	TENDER

NOT FOR
CONSTRUCTION

ISSUED FOR TENDER

CILAIRE ELEMENTARY
MODULAR DAYCARE STUDIO
SITE WORKS

25 CILAIRE DRIVE, NANAIMO, BC

SCHOOL DISTRICT 68 NANAIMO/LADYSMITH

**HEROLD
ENGINEERING**
3701 Shenton Rd, Nanaimo, BC V9T 2H1
Tel: 250-751-8558 Fax: 250-751-8559
Email: mail@heroldengineering.com

©Copyright reserved. This drawing remains the exclusive property of Herold Engineering Limited and may not be reused or reproduced without written consent of Herold Engineering Limited.

EROSION & SEDIMENT CONTROL PLAN	
DESIGNED SMJ	ENGINEER'S SEAL Permit to Practice No. 1000201
DESIGN REVIEW PGR	
DRAFTED GV	
DRAFTING REVIEW PGR	
PROJECT No. 0016-352	CLIENT DRAWING No.
SCALE H: 1:250 V: N/A	PERMIT No.
HEL DRAWING No. C06	REVISION 6 OF 6 D