



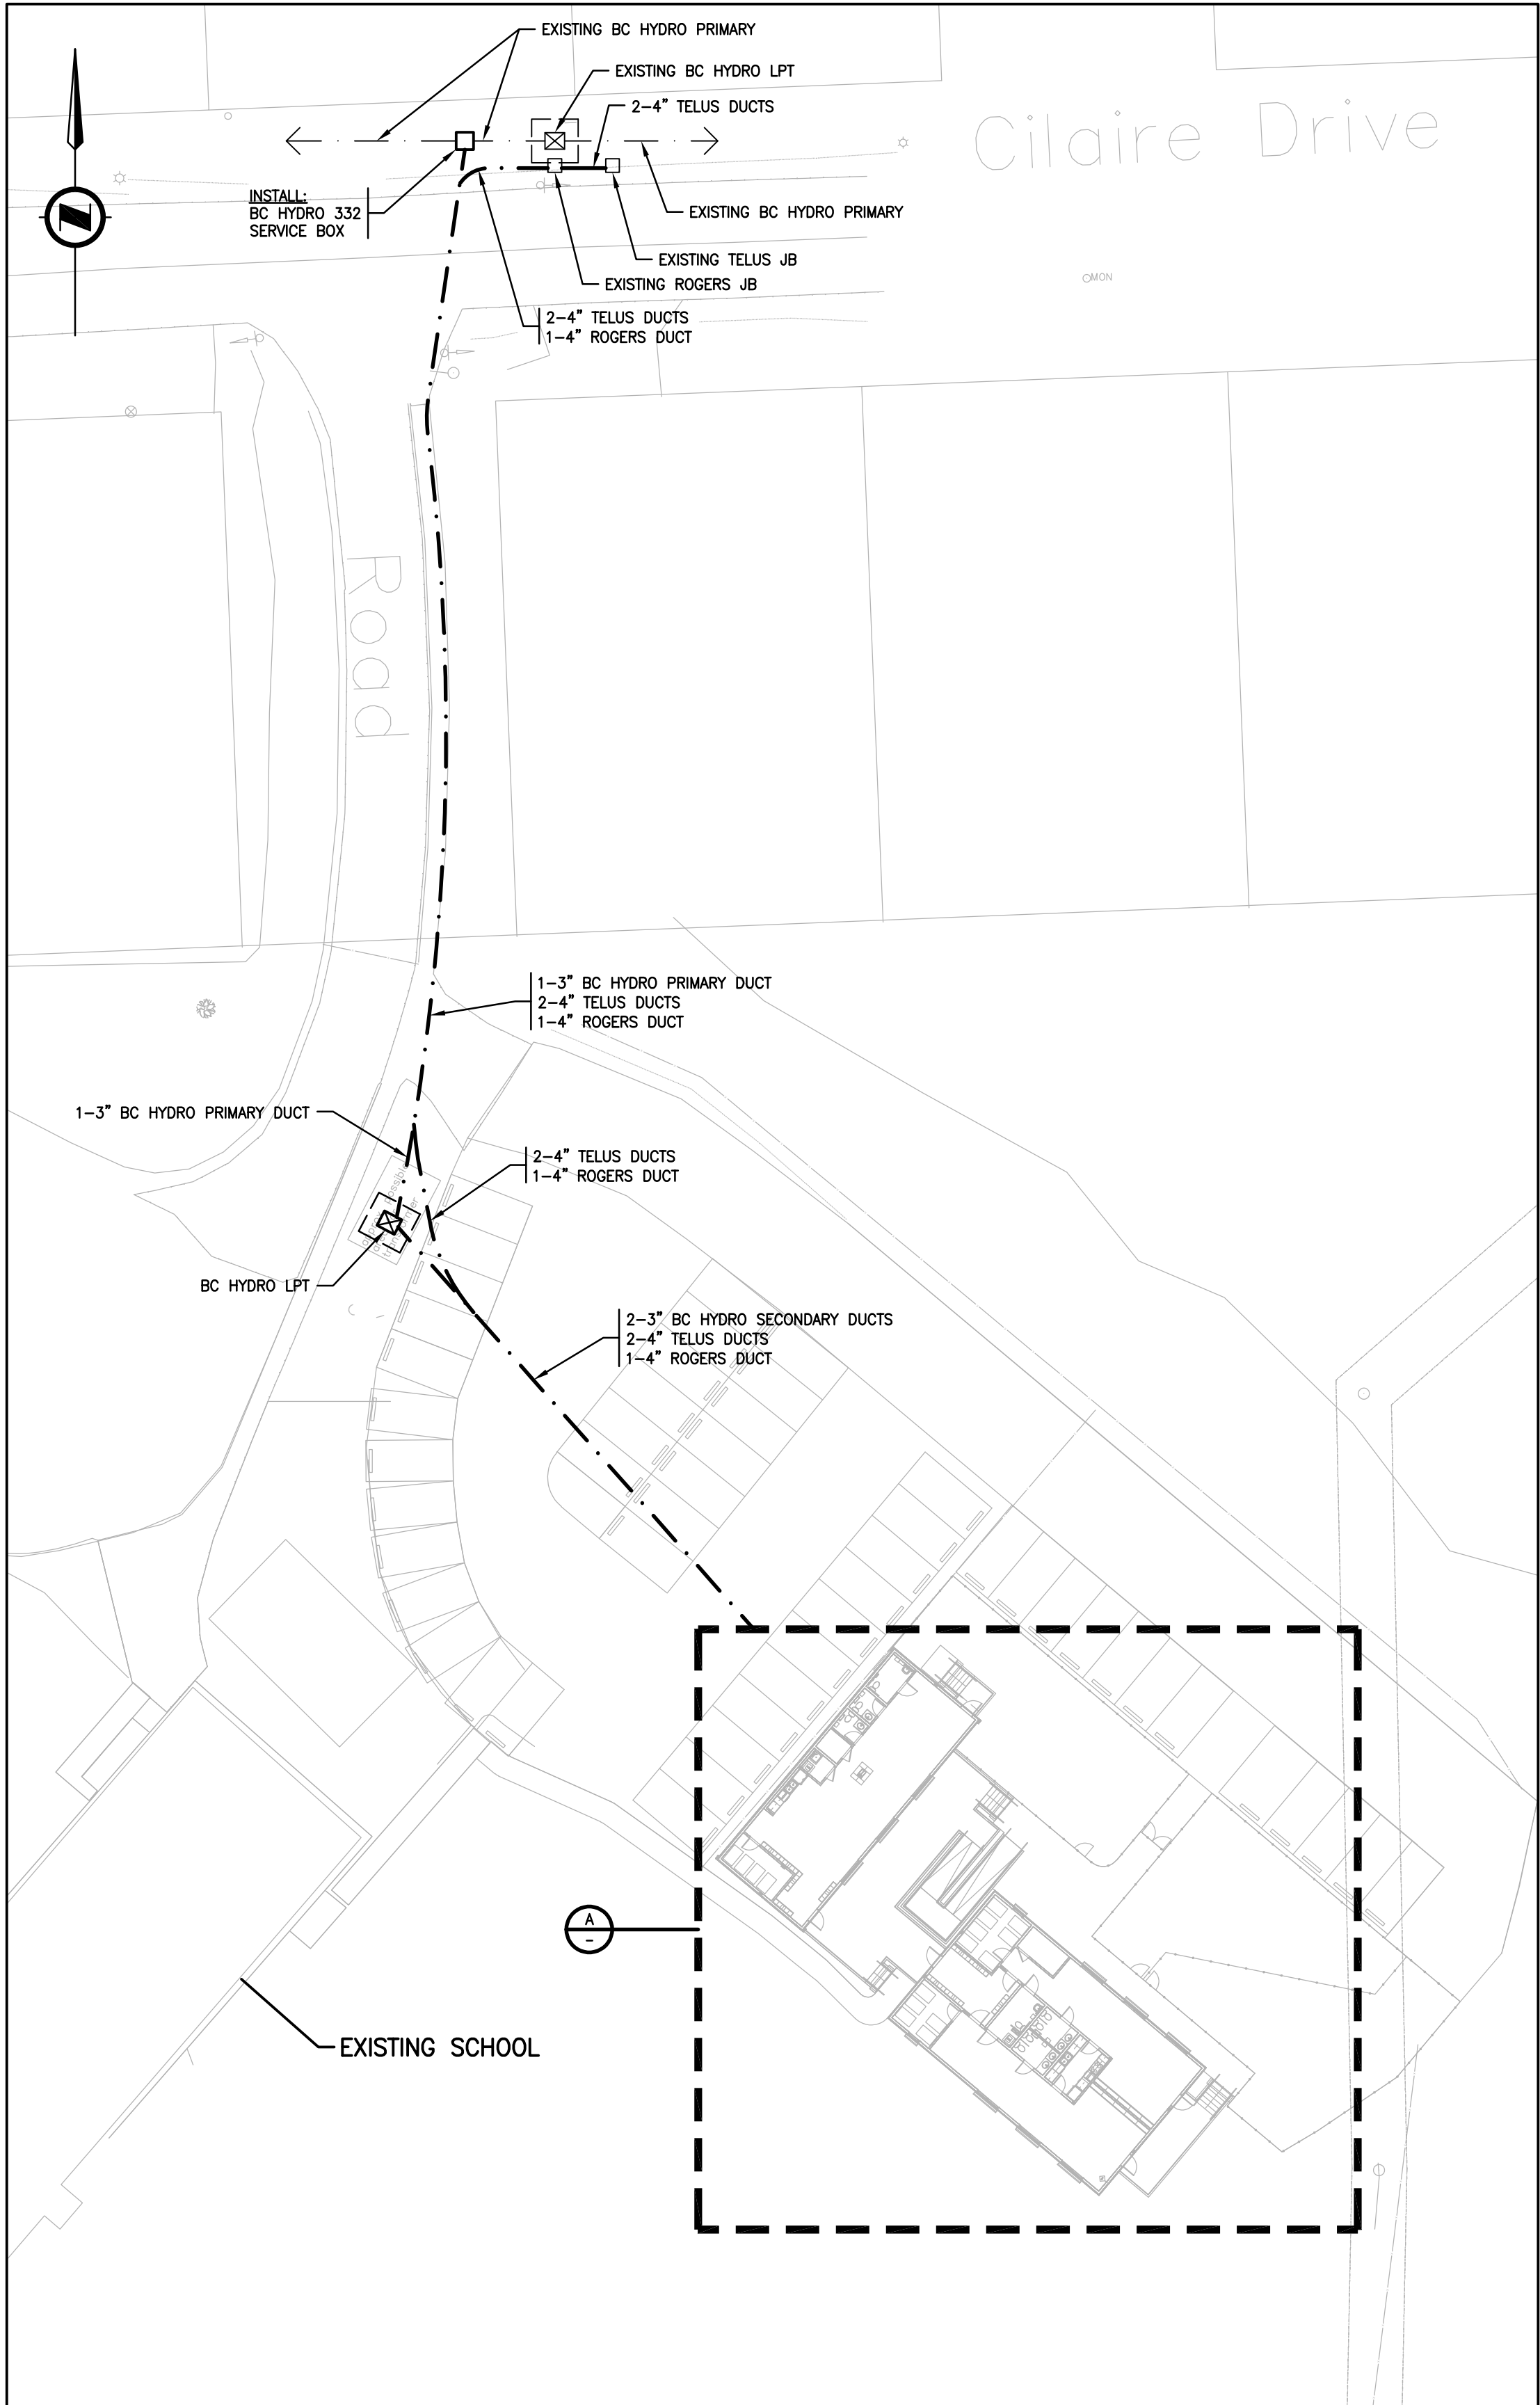

OVERALL SITE PLAN
SCALE: 1:350

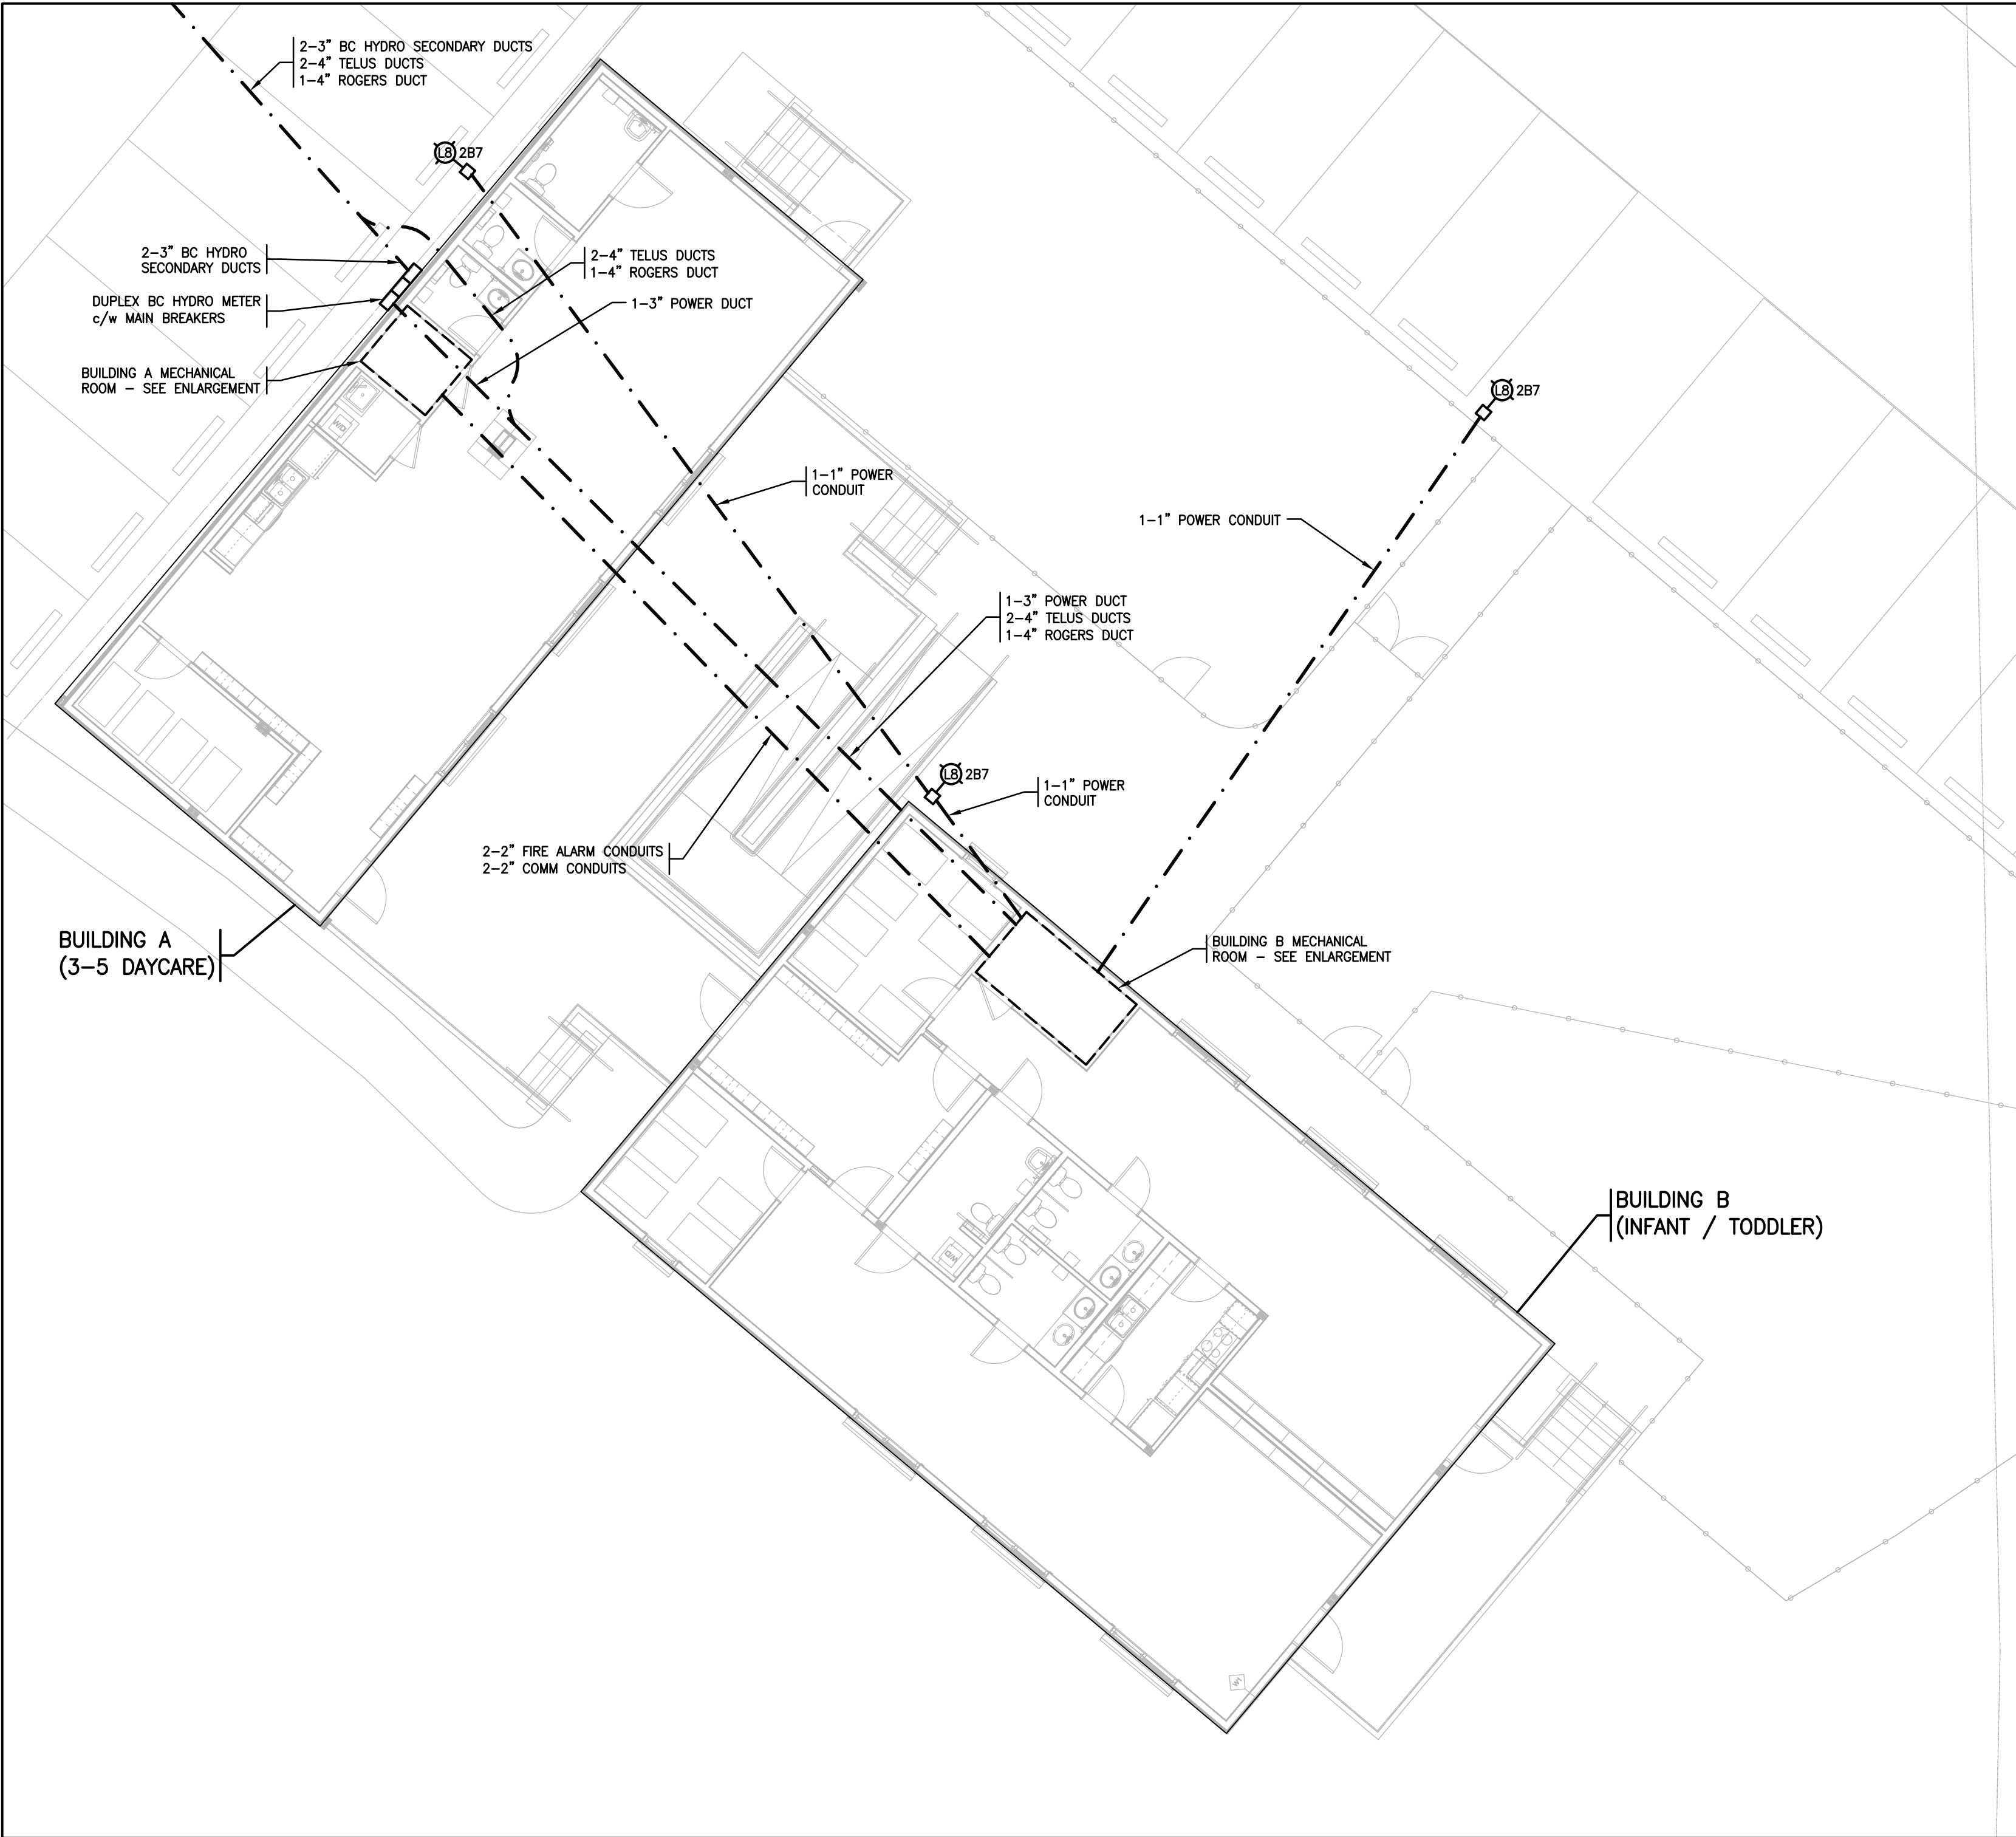

A SITE PLAN ENLARGEMENT
SCALE: 1:100

UTILITY NOTES:

1. CONTRACTOR TO ARRANGE A PRE-JOB SITE REVIEW WITH BC HYDRO PRIOR TO ANY INSTALLATION OF BC HYDRO INFRASTRUCTURE.
2. REFER TO BC HYDRO, TELUS AND ROGERS "ISSUED FOR CONSTRUCTION" DRAWINGS FOR EXACT ROUTING/PLACEMENT OF DUCTS, PADS, GROUNDING, PULL BOXES, ETC.

GENERAL NOTE:

ALL ITEMS IN BOLD ARE NEW UNLESS NOTED OTHERWISE.

NO.	DATE	TITLE
3	JAN 14 2026	ISSUED FOR TENDER - CIVIL ONLY
2	JUN 19 2025	ISSUED FOR PERMIT
1	MAY 08 2025	ISSUED FOR UTILITY COORDINATION
REVISION		


RB ENGINEERING LTD.
ELECTRICAL CONSULTING ENGINEERS
#4 1850 NORTHFIELD ROAD TEL 250-756-4444
NANAIMO, BC, V9S 3B3 RBENGINEERING.CA
EGBC PERMIT #1001907
THIS DRAWING IS SOLELY INTENDED TO BE USED FOR THE PURPOSE OF THE DRAWING REVISION TITLE AND SHALL NOT BE USED FOR ANY OTHER PURPOSE




PROJECT
CILAIRE ELEMENTARY DAYCARE MODULAR

TITLE
SITE PLAN ELECTRICAL LAYOUT

PROJECT NO. 22-4043	SEAL
DATE APRIL, 2025	
SCALE AS SHOWN	

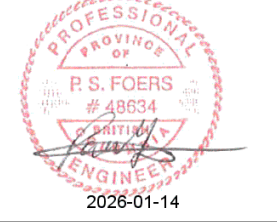


DRAWING NO.
E1.01

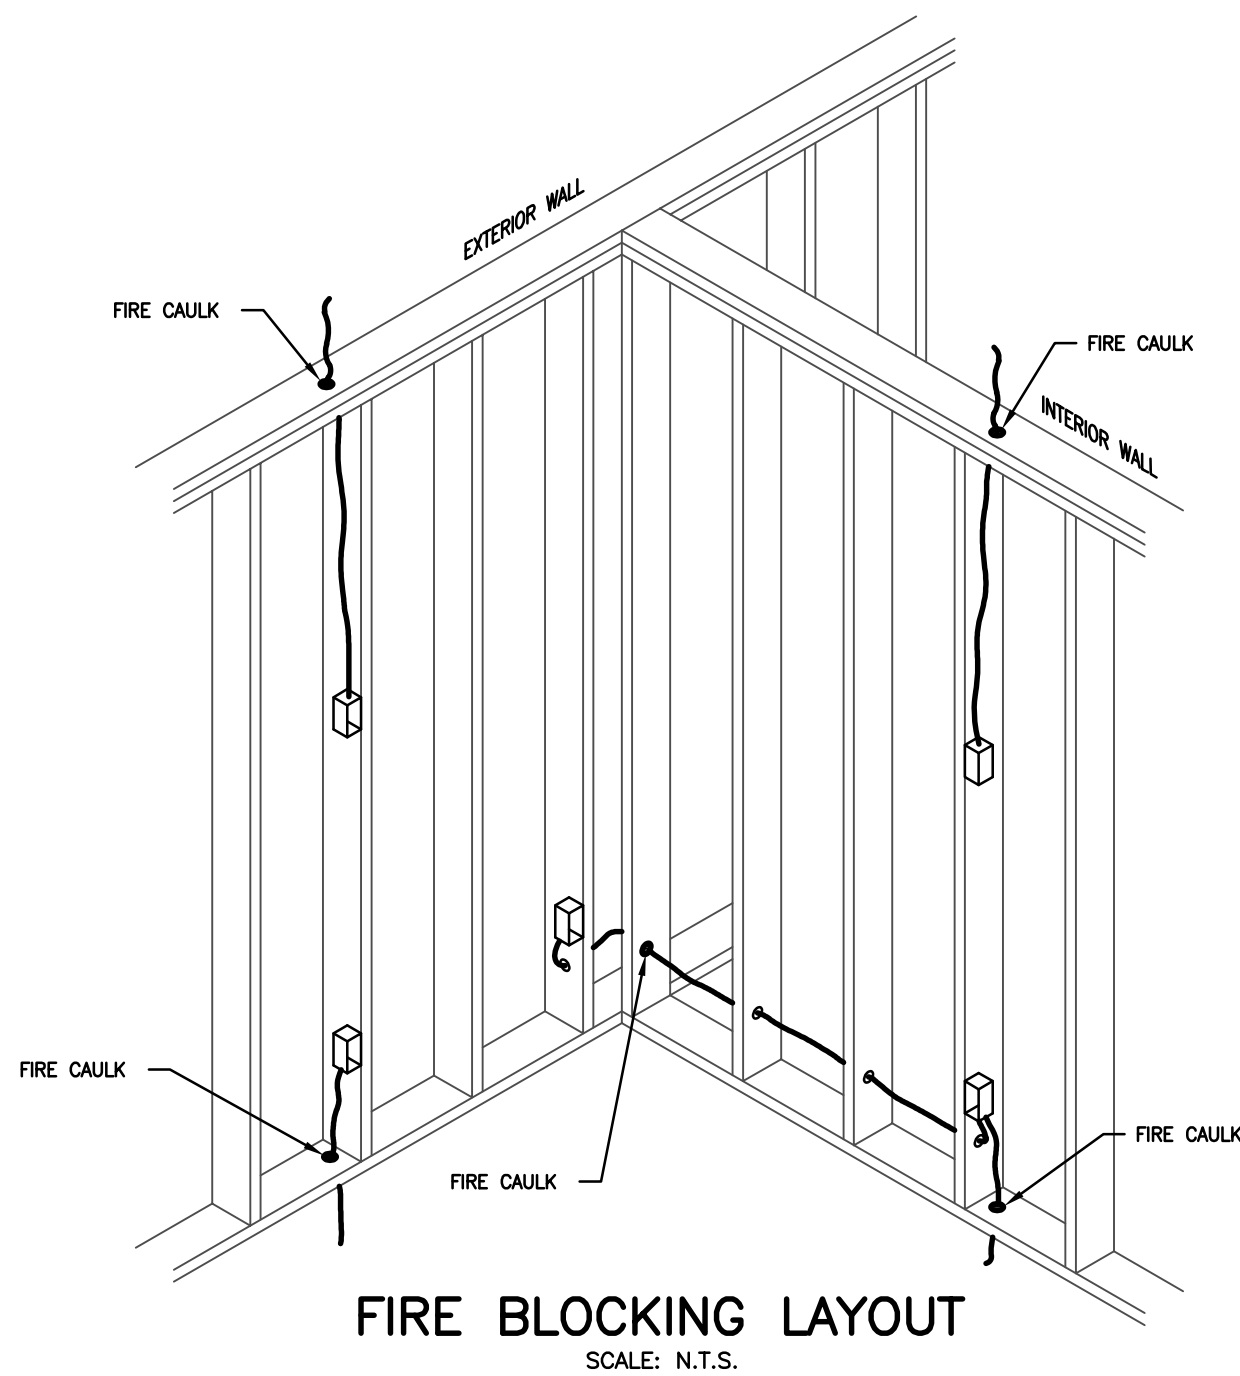

FIRE BLOCKING NOTES:

1. SEAL ALL VERTICAL ELECTRICAL PENETRATIONS THROUGH TOP AND BOTTOM FRAMING PLATES.
2. SEAL ALL HORIZONTAL ELECTRICAL PENETRATIONS FROM INTERIOR WALLS TO EXTERIOR WALLS.
3. THIS DIAGRAM DEMONSTRATES MAJORITY OF REQUIRED FIRE BLOCK SCENARIOS. REFER TO BUILDING CODE SECTION 3.1.11 FOR ALL REQUIREMENTS.
4. ELECTRICAL CONTRACTOR IS RESPONSIBLE TO NOTIFY RB ENGINEERING PRIOR TO COVER-UP OF ELECTRICAL WIRING REGARDLESS IF CONTRACTOR DOES FIRE BLOCKING WORK OR NOT.

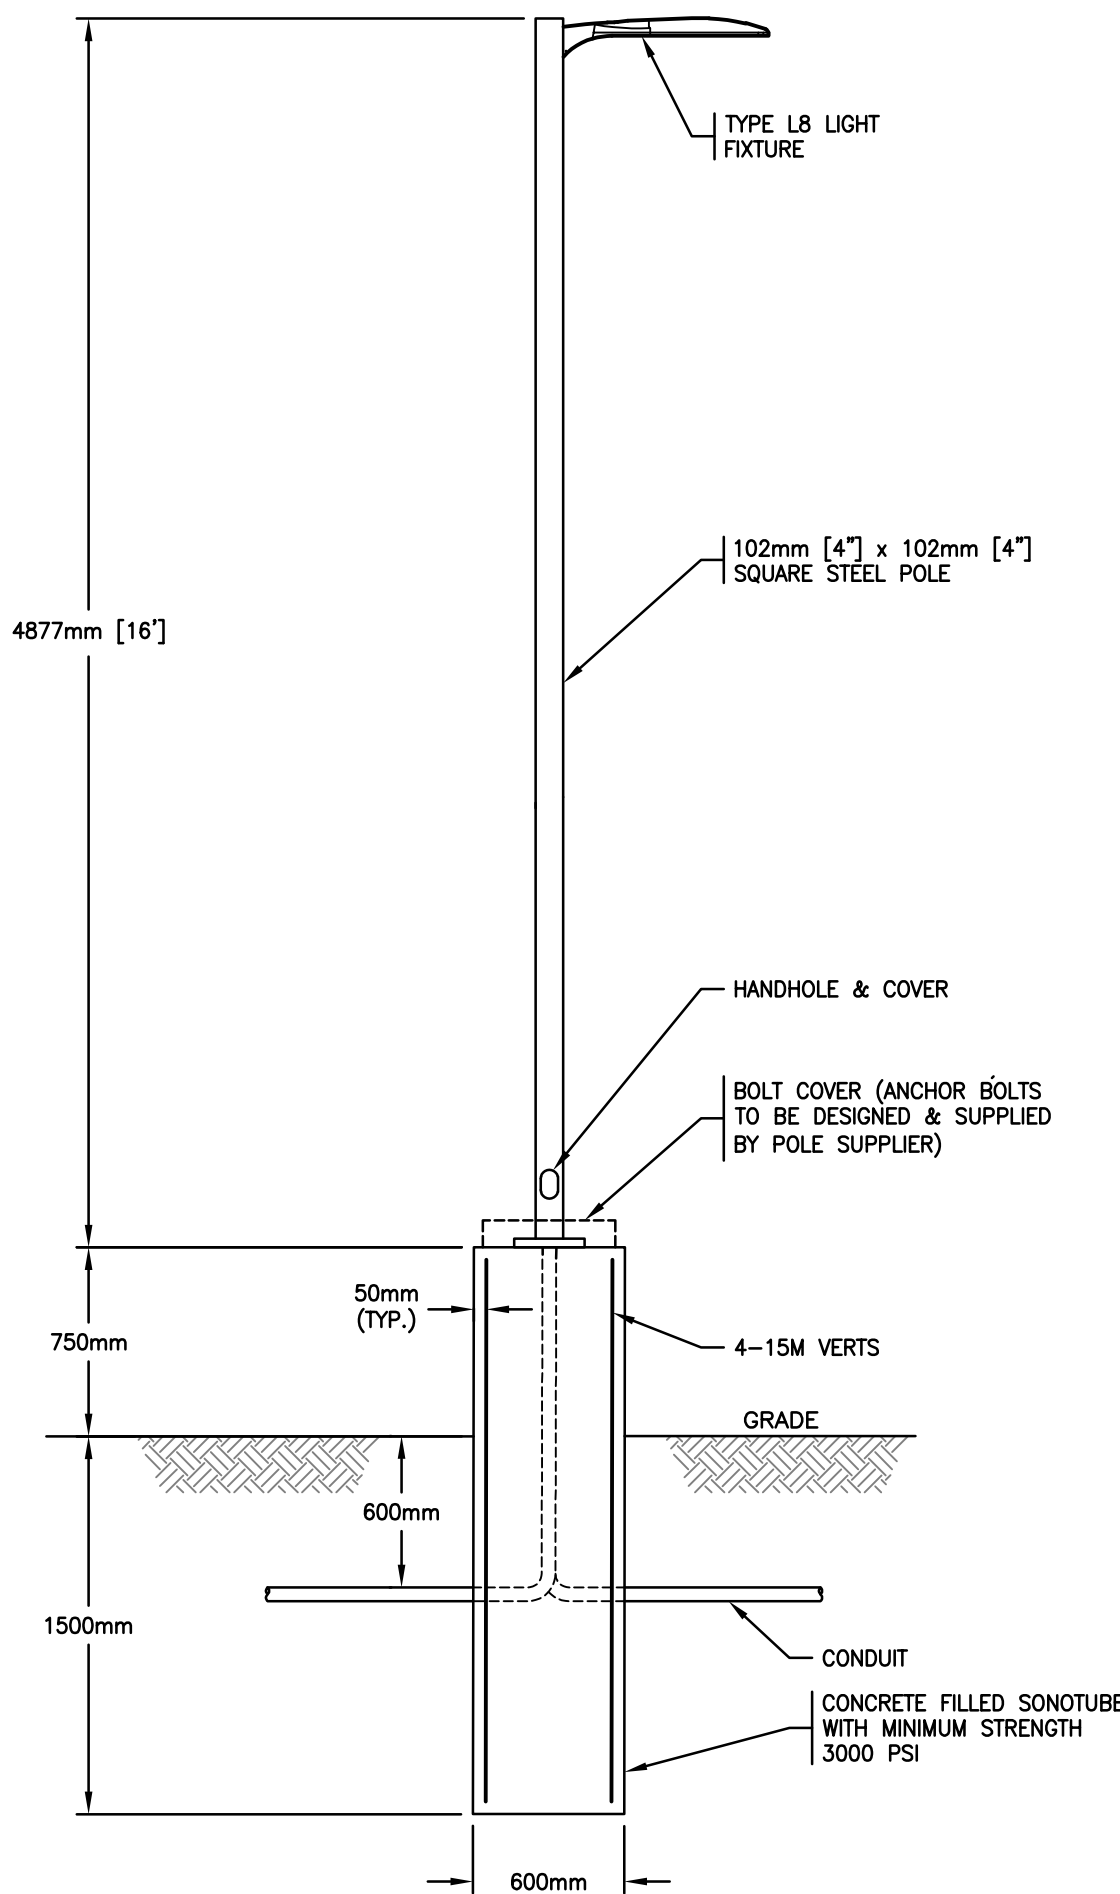

PARKING LOT LUMINAIRE (TYPE L8)
SCALE: N.T.S.

2	JAN 14 2026	ISSUED FOR TENDER – CIVIL ONLY
1	JUN 19 2025	ISSUED FOR PERMIT
NO.	DATE	TITLE
REVISION		

RB ENGINEERING LTD
ELECTRICAL CONSULTING ENGINEERS
#4 1850 NORTFIELD ROAD TEL 250-756-4444
NANAIMO, BC, V9S 3B3 RBENGINEERING.CA
EGBC PERMIT #1001907
THIS DRAWING IS SOLELY INTENDED TO BE USED FOR THE PURPOSE OF THE DRAWING REVISION TITLE AND SHALL NOT BE USED FOR ANY OTHER PURPOSE

CLIENT
**NANAIMO LADYSMITH**
PUBLIC SCHOOLS

PROJECT
CILAIRE ELEMENTARY
DAYCARE MODULAR

TITLE
ELECTRICAL
DETAILS
SHEET 2 OF 2

PROJECT NO. 22-4043	
DATE APRIL, 2025	
SCALE N.T.S.	

DRAWING NO.
E3.02

